


OVERALL URBAN DESIGN · ONE PUBLIC BASELINE, THREE RECEIPT LANDMARKS


OVERALL URBAN DESIGN · PUBLIC BASELINE LINKS THREE RECEIPT LANDMARKS

City fabric, spine, stations, wings and stitches only; S7 detail belongs to the key-area figure

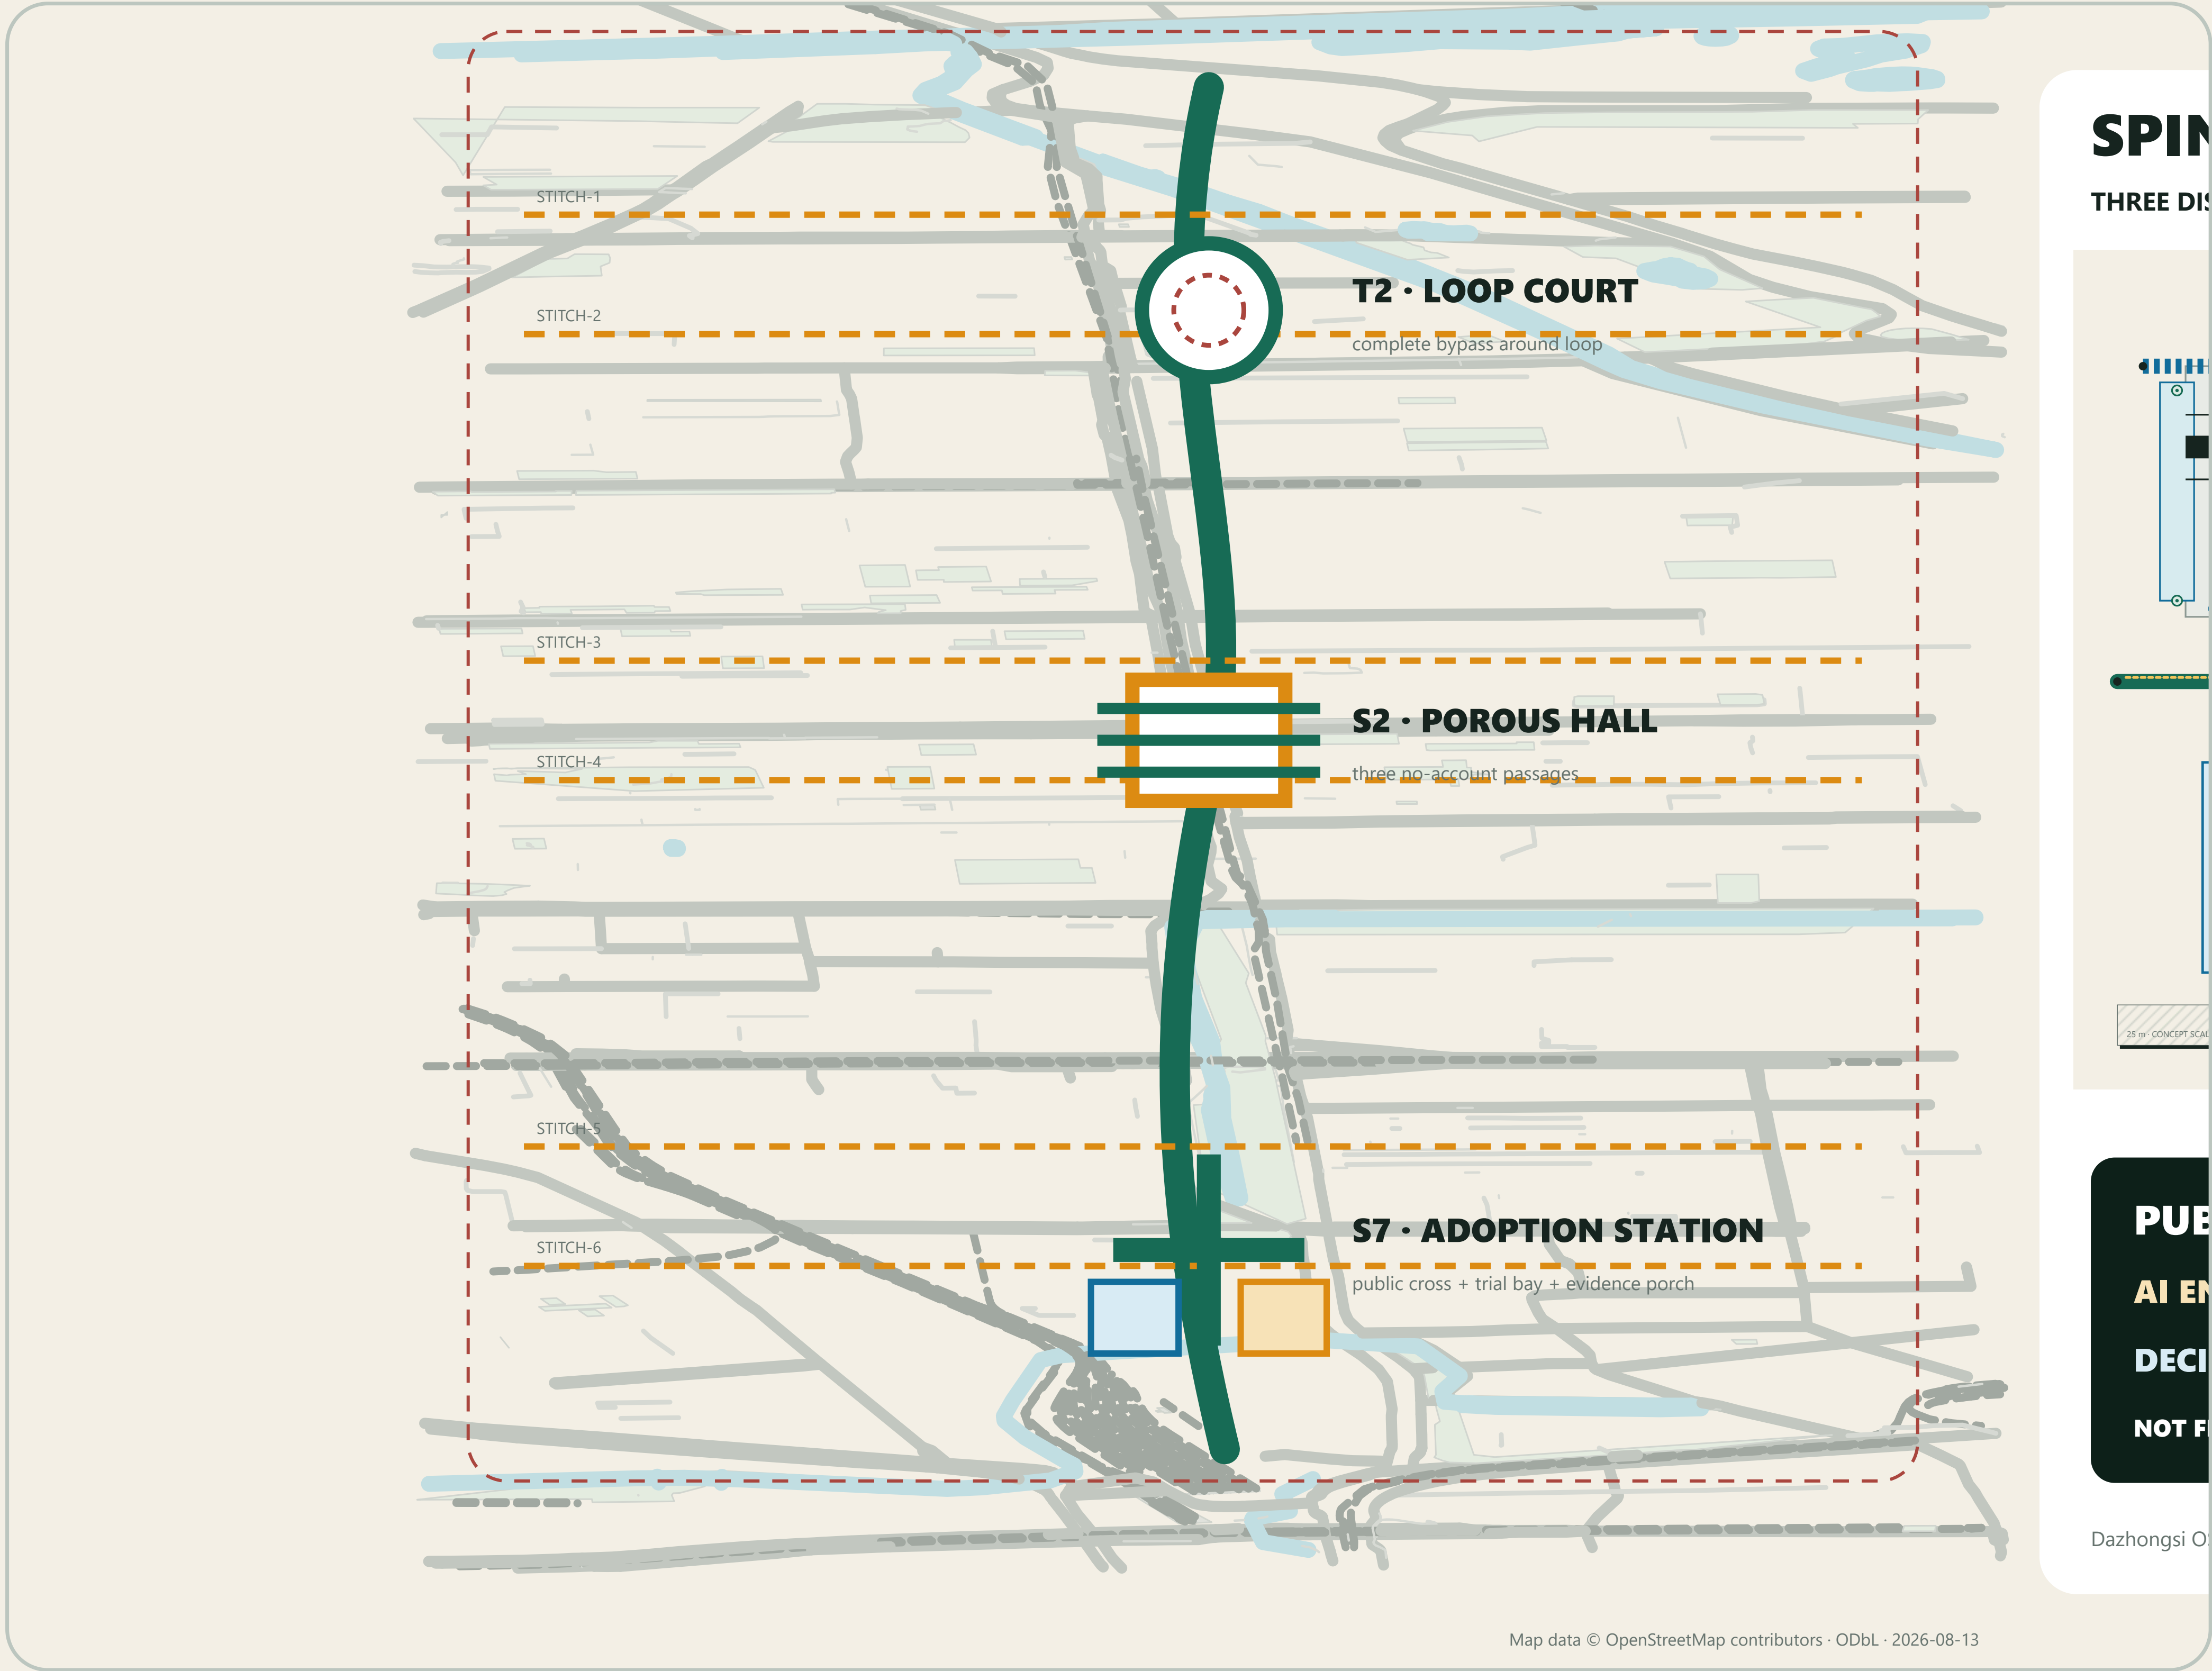

Map data © OpenStreetMap contributors · ODbL · 2026-08-13 · provisional boundary and concept layout pending official base

THREE SPATIAL ARCHETYPES

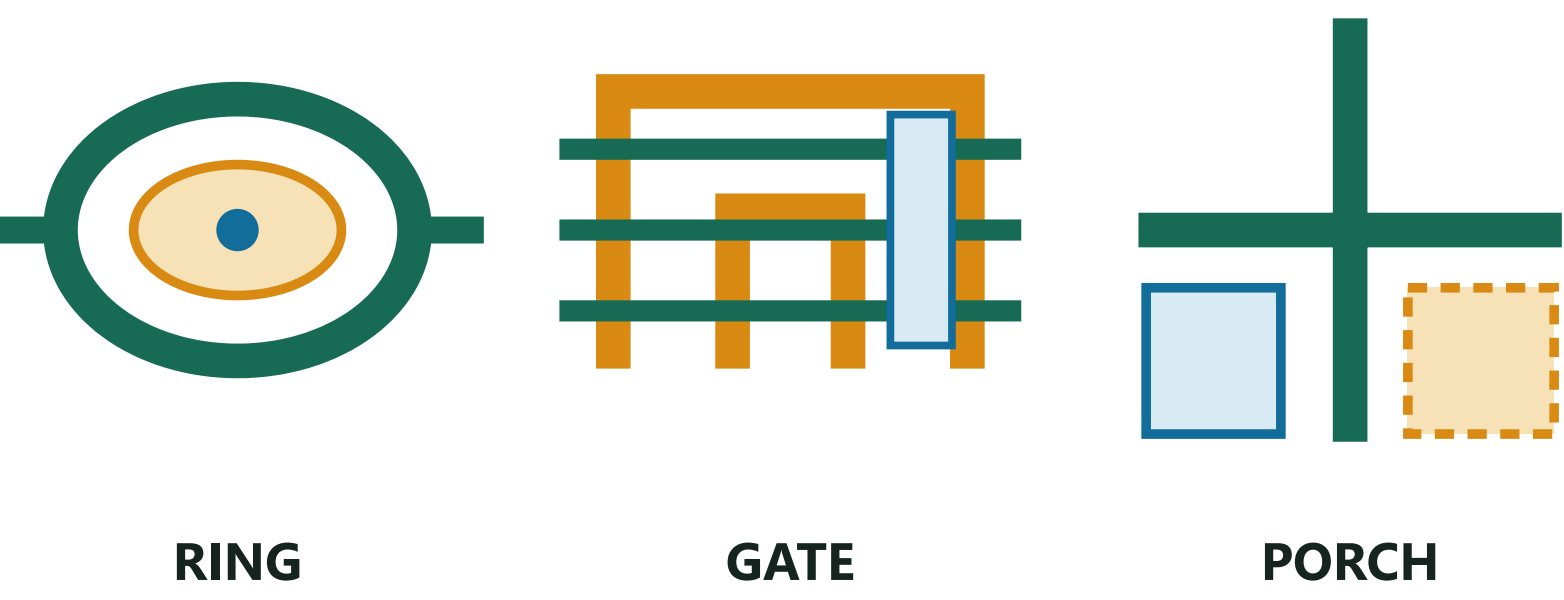

CIVIC ADOPTION COMPILER

- 01 COMPLETE PUBLIC ROUTE
- 02 TRIGGERABLE STOP
- 03 REVIEWABLE RECEIPT


12 × 7 = 84 / 84 PASS

T0 SYNTHETIC CONTRACT VERIFIED

FIELD PERFORMANCE · UNKNOWN

GROUND-FLOOR USE + PERMANENT / TEMPORARY OCCUPATION BAND

Land-use judgement shifts from coloured parcels to enterable ground floors, public edges and timed occupation

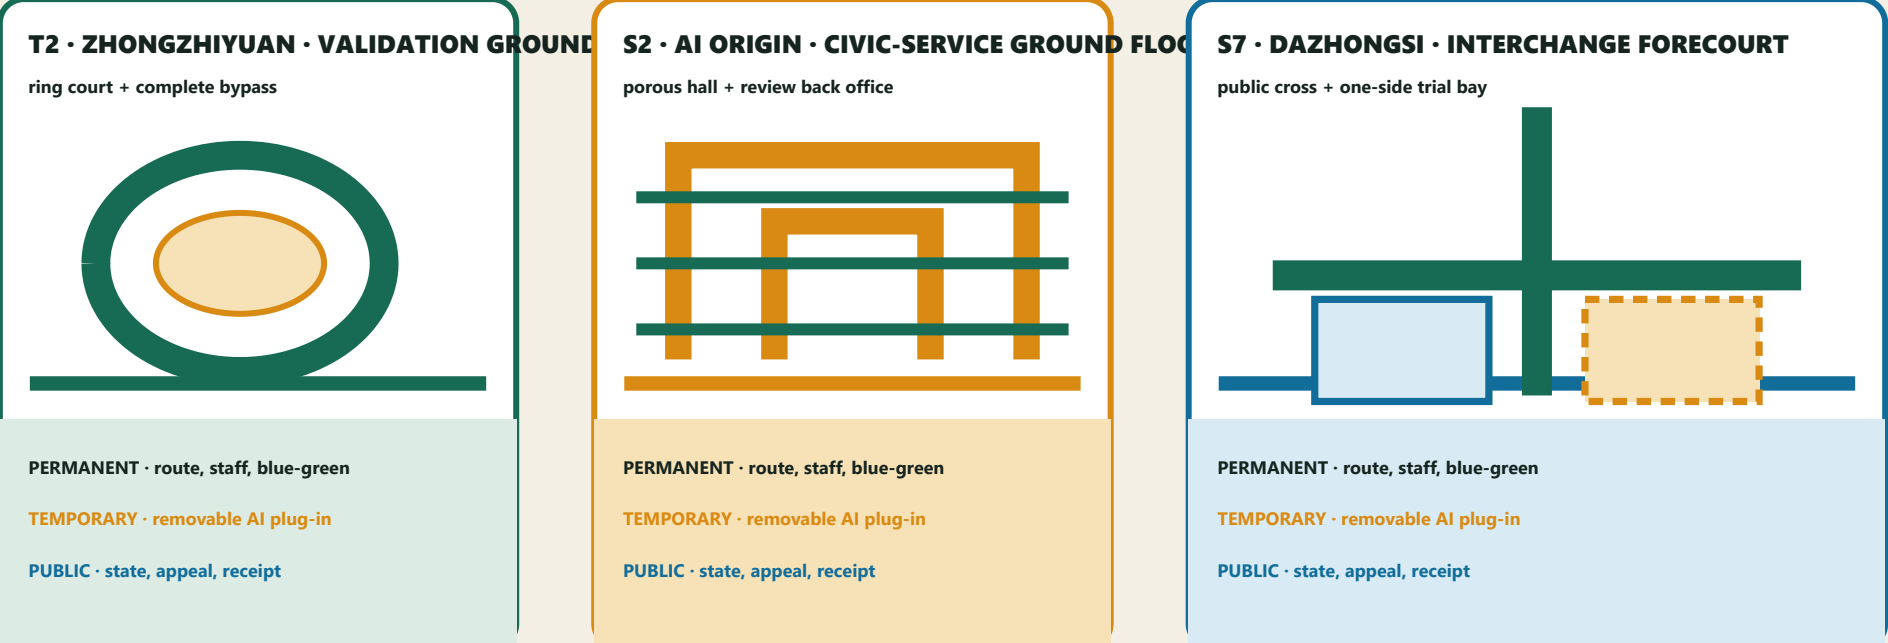

RENEWAL ORDER · PUBLIC ROUTE → GROUND EDGE → REMOVABLE PLUG-IN → FIELD RECEIPT

PERMANENT BASELINE independent all day	PUBLIC EVIDENCE human decision + appeal	TIMED TRIAL permits complete before opening	FAILURE EXIT restore ordinary use
--	---	---	---

Concept ground floor and occupation relationships, not statutory land use zoning buildings or approval

CIVIC ADOPTION COMPILER

01 · COMPLETE PUBLIC ROUTE

02 · TRIGGERABLE STOP


03 · REVIEWABLE RECEIPT

84 SYNTHETIC · FIELD UNKNOWN

THREE SPATIAL TYPES • S7 FOUR SCALES PLUS 1:50 ASSEMBLY NODE


THREE LANDMARKS AT A COMPARABLE SCALE • RING, GATE AND PORCH READ WITHOUT TITLES

T2 • ZHONGZHIYUAN • VERIFICATION RING

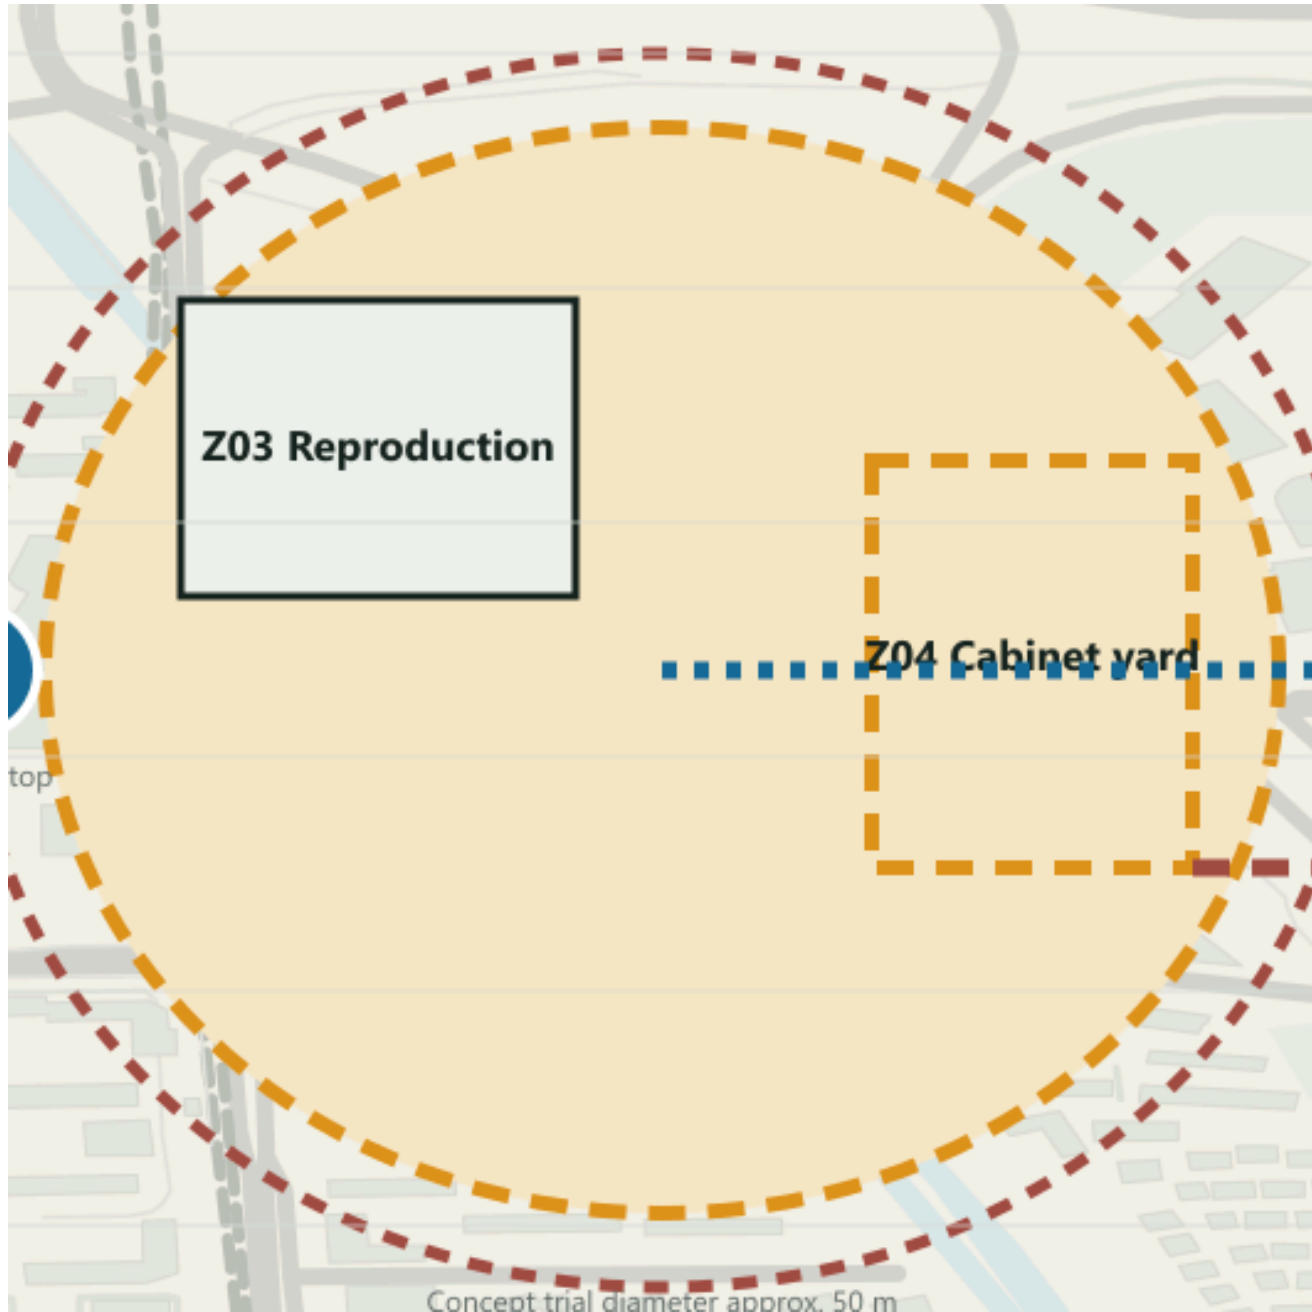


Concept trial diameter approx: 50 m

T2 • Controlled robot-pedestrian-accessibility test • 1:200

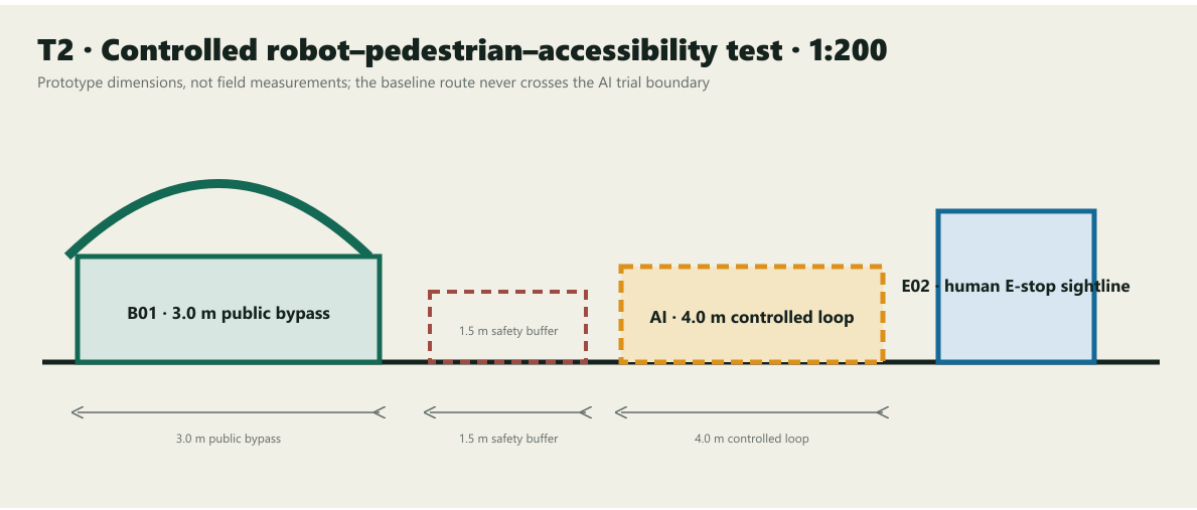


S2 • AI ORIGIN • TRANSLATION GATE

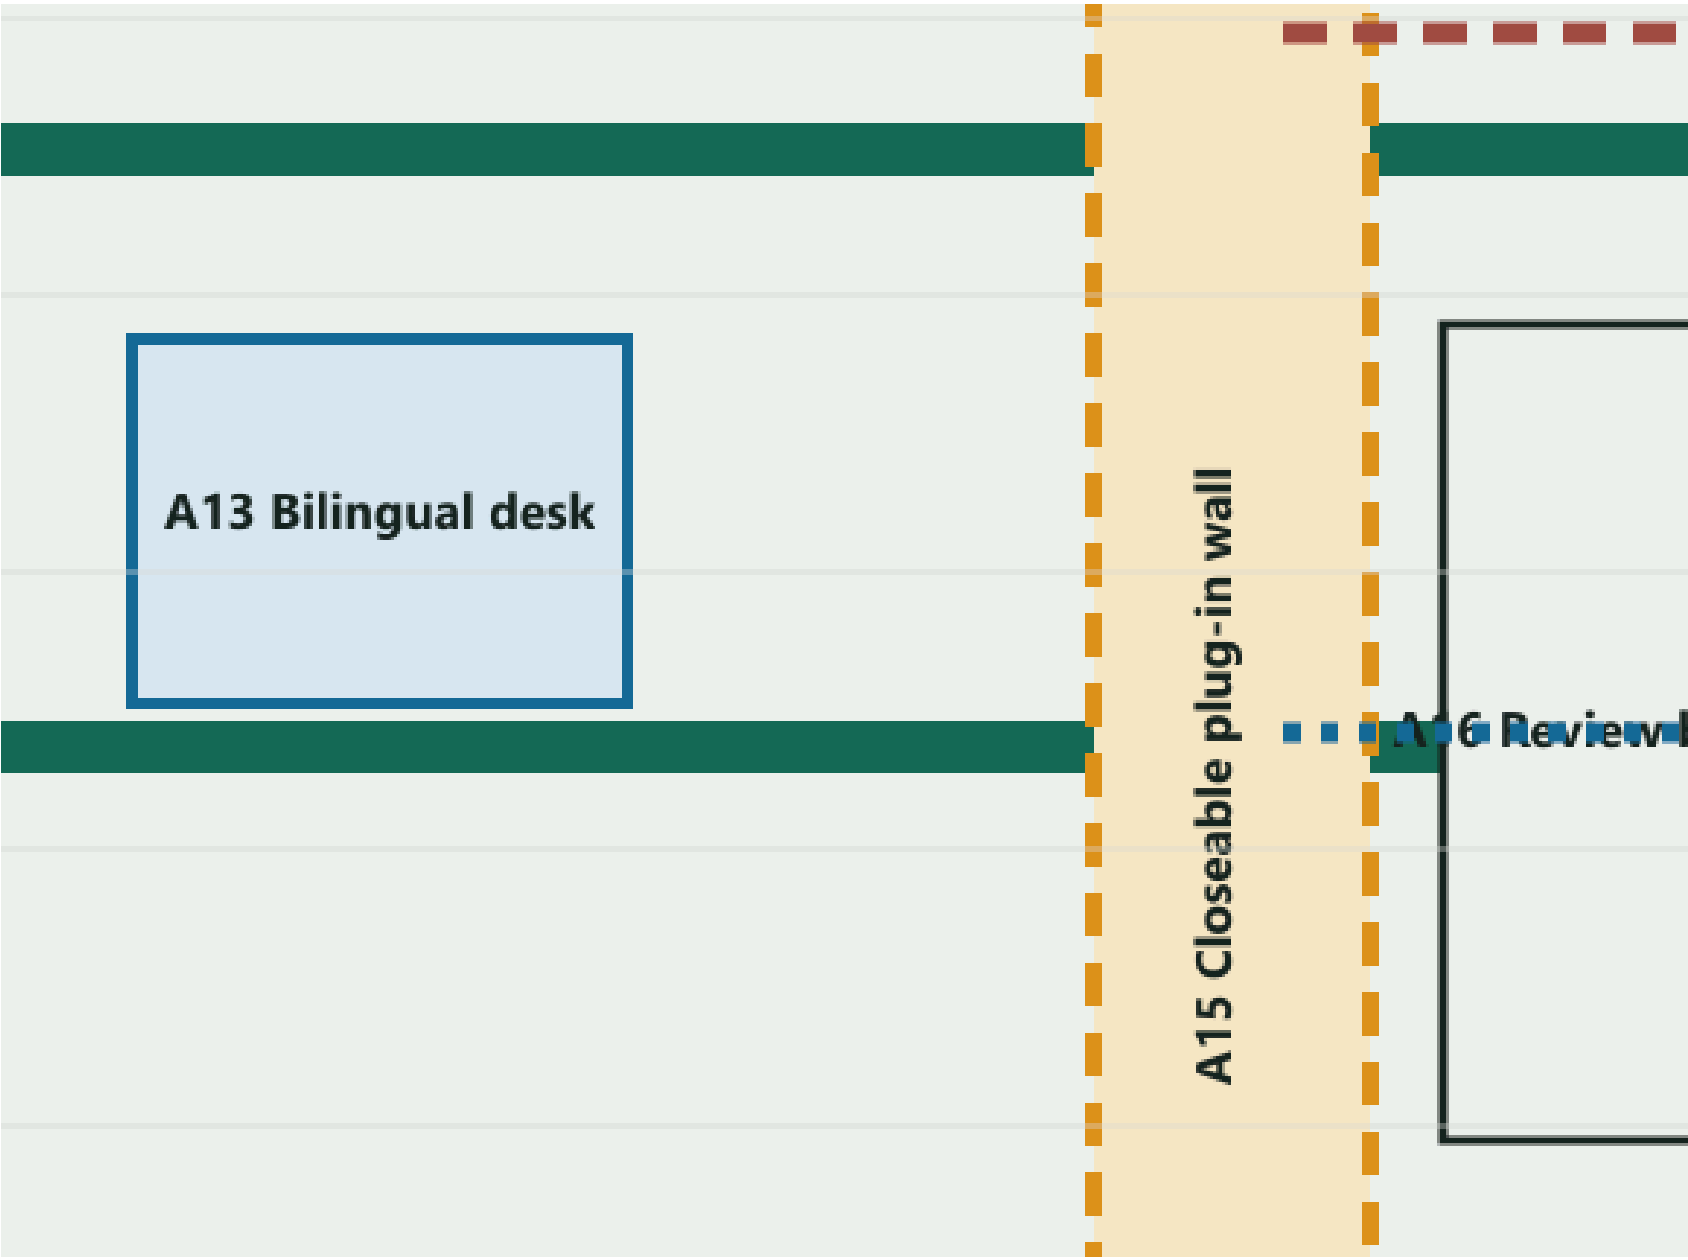


6 Review

S2 • International arrival and civic-service navigation • 1:200

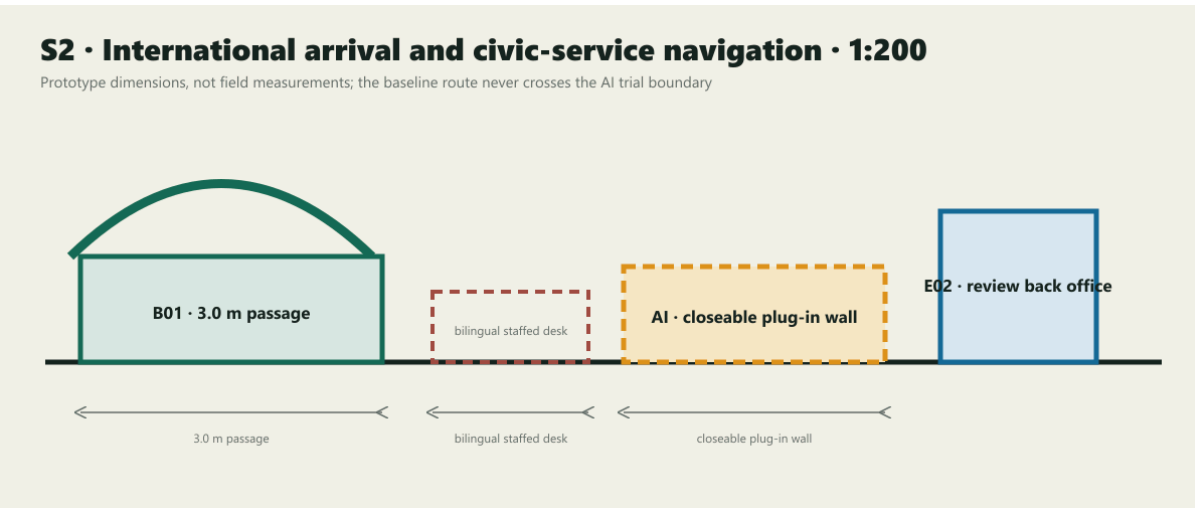


S7 • DAZHONGSI • RECEIPT PORCH

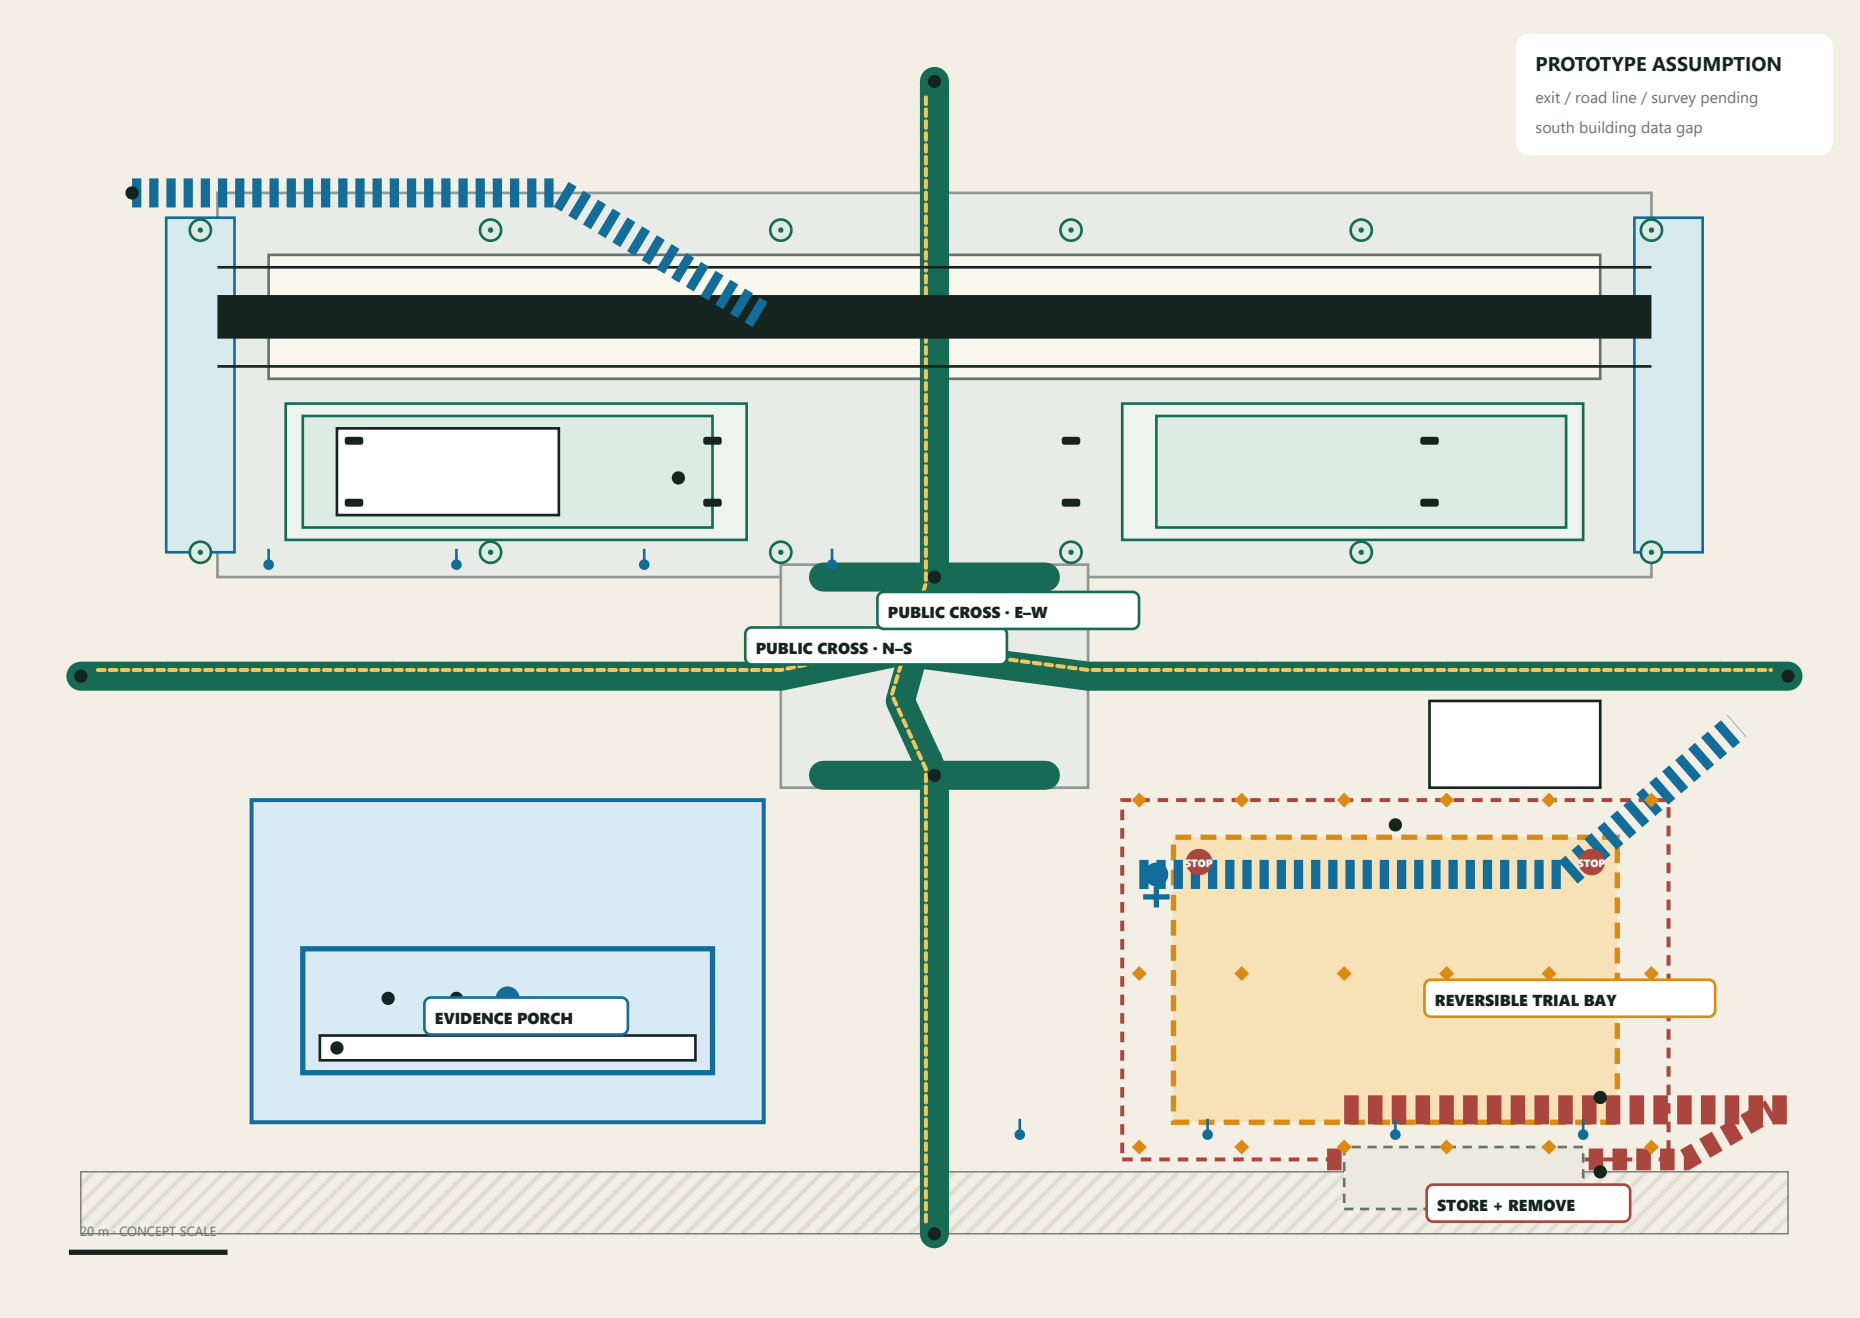

PROTOTYPE ASSUMPTION
exit / road line / survey pending
reach building data gap


1:200 SECTION • THE TRIAL NEVER CAPTURES THE PUBLIC ROUTE

1:200 SECTION • THE TRIAL NEVER CAPTURES THE PUBLIC ROUTE

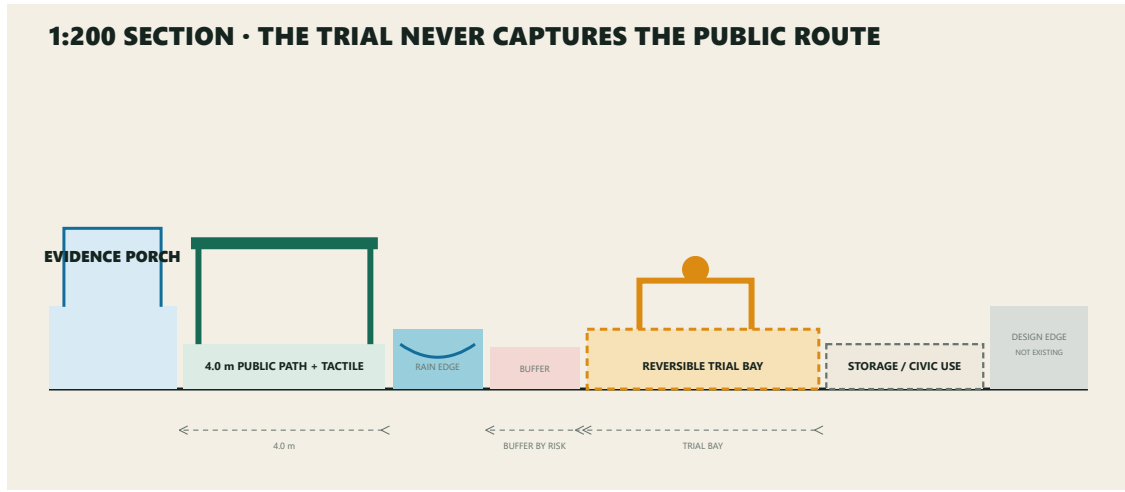

S7 • 1:50 ASSEMBLY NODE

ramp / tactile • removable barrier • evidence plate • temporary power • rain edge

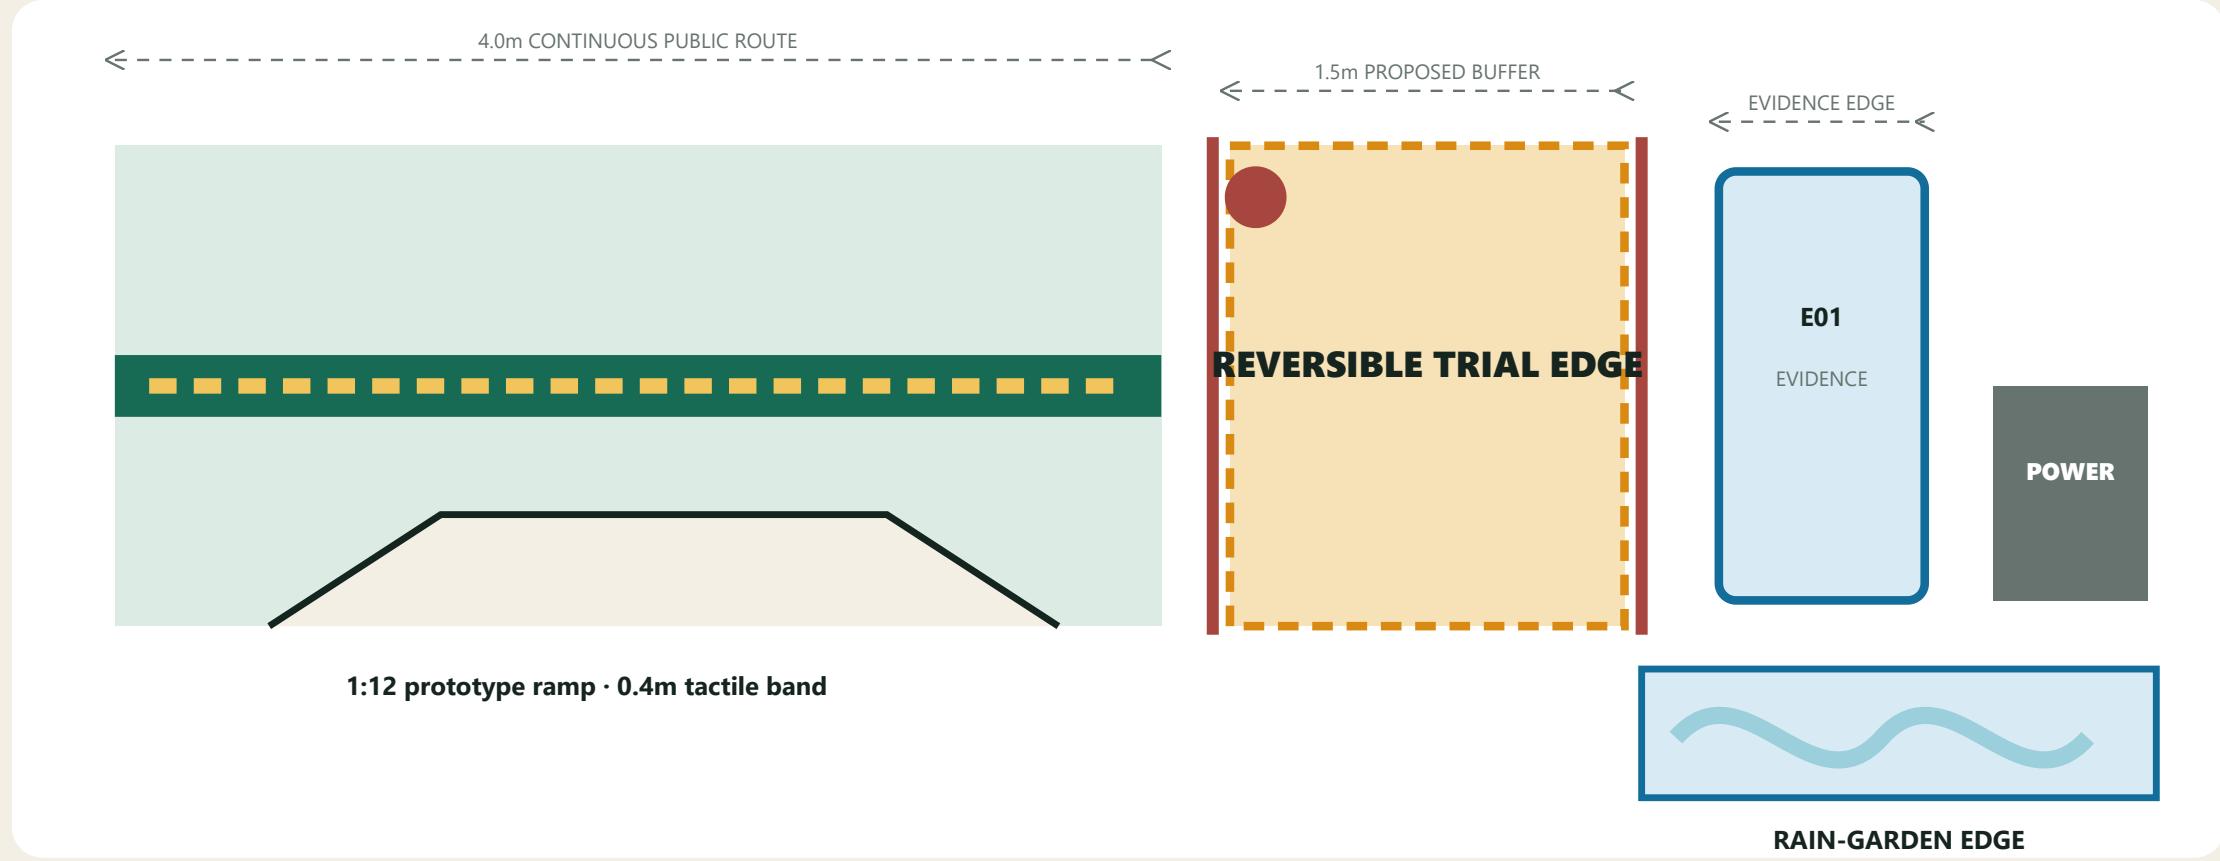

4.0m CONTINUOUS PUBLIC ROUTE

1.5m PROPOSED BUFFER

EVIDENCE EDGE

REVERSIBLE TRIAL EDGE

E01 EVIDENCE

POWER


1:12 prototype ramp • 0.4m tactile band

RAIN-GARDEN EDGE

- B01 - baseline first
- A01 - plug-in on one side
- E01 - decision publicly visible
- E02 - E-stop outside route

All dimensions are reviewable prototype assumptions pending survey and professional accessibility, fire, utility and equipment review.

ASSEMBLY AXON • ROUTE, BAY, PORCH, BLUE-GREEN EDGE

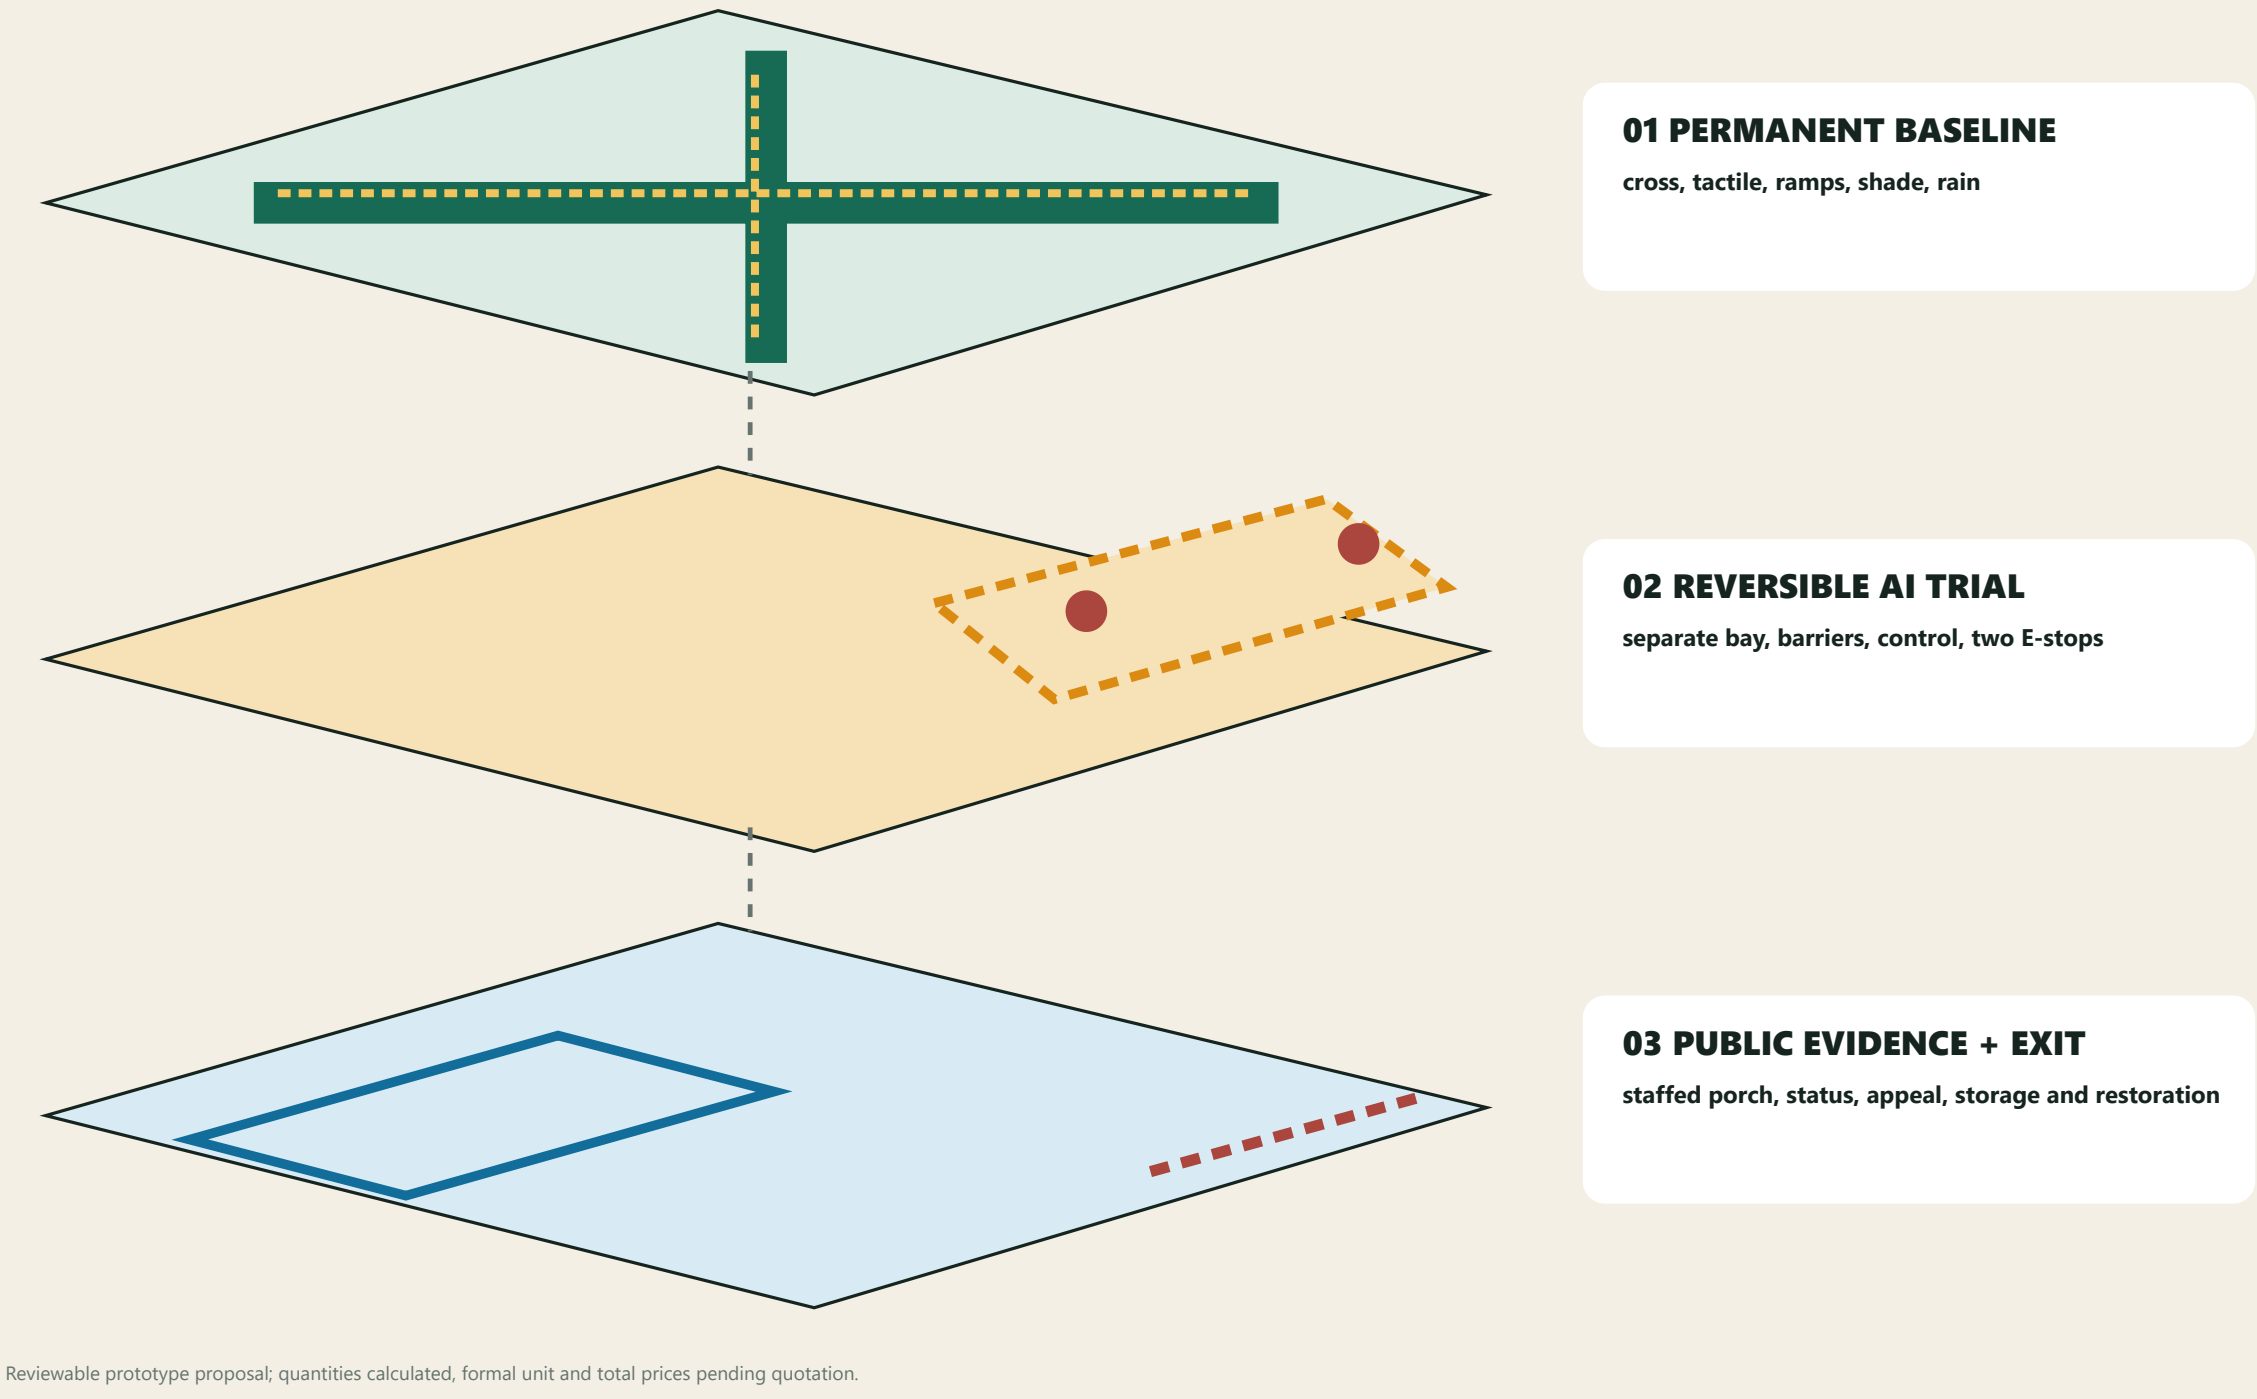


01 PERMANENT BASELINE
cross, tactile, ramps, shade, rain

02 REVERSIBLE AI TRIAL
separate bay, barriers, control, two E-stops

03 PUBLIC EVIDENCE + EXIT
staffed porch, status, appeal, storage and restoration

Reviewable prototype proposal; quantities calculated; formal unit and total prices pending quotation.

ALLOWED STATE MACHINE • ILLEGAL JUMPS BLOCK PUBLICATION

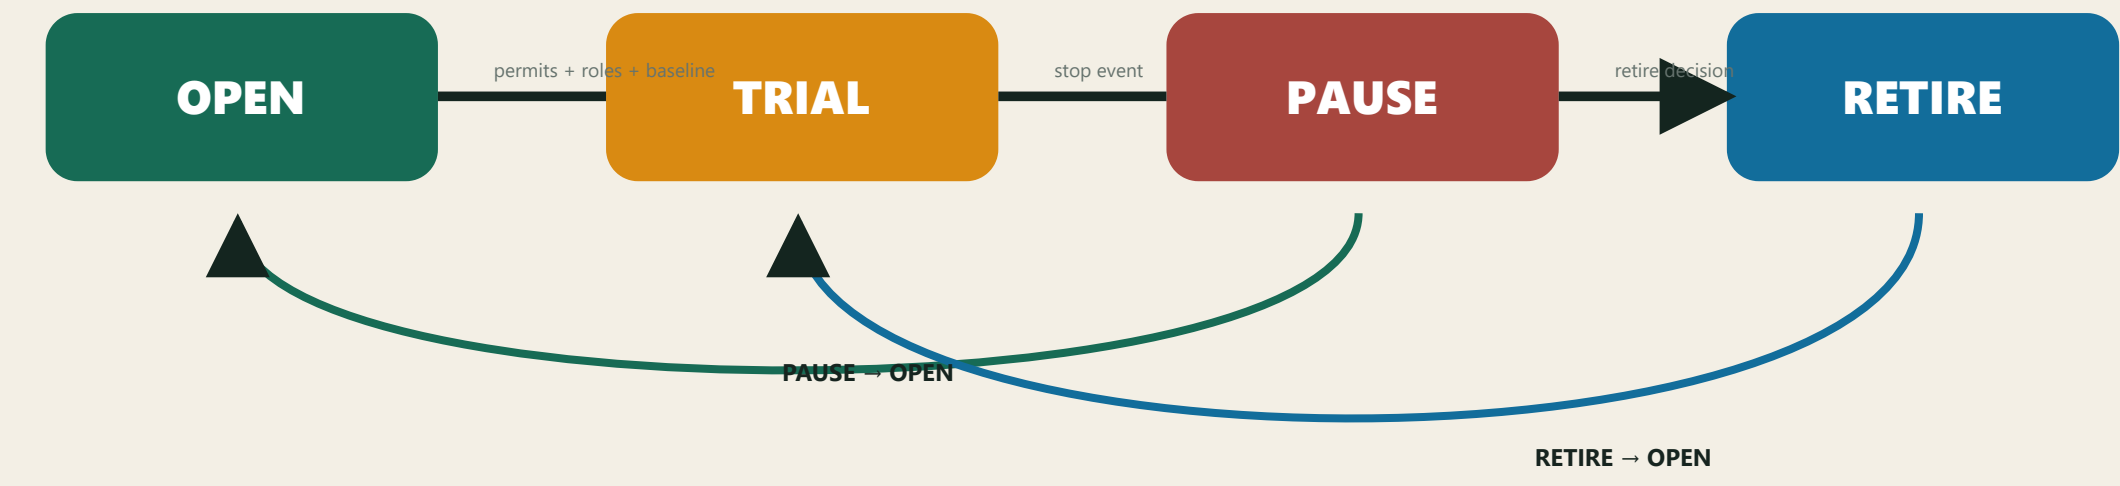

OPEN

TRIAL

PAUSE

RETIRE

PERMITS + EXIT

STOP EVENT

PAUSE - OPEN

RETIRE - OPEN

All scales are prototype proposals; existing conditions, interfaces and permits await formal data and professional review.


T2 ring • S2 gate • S7 porch • dimensions pending survey and professional review

T0 SYNTHETIC VERIFIED • E2 DOCUMENTED • NOT FIELD-RUN

CIVIC ADOPTION COMPILER • RULES COMPILE FIRST, FIELD PROVES LATER

CIVIC ADOPTION COMPILER • 84 SYNTHETIC CASES, PERMIT GATES + FIELD UNKNOWNNS

ALLOWED STATE MACHINE • ILLEGAL JUMPS BLOCK PUBLICATION

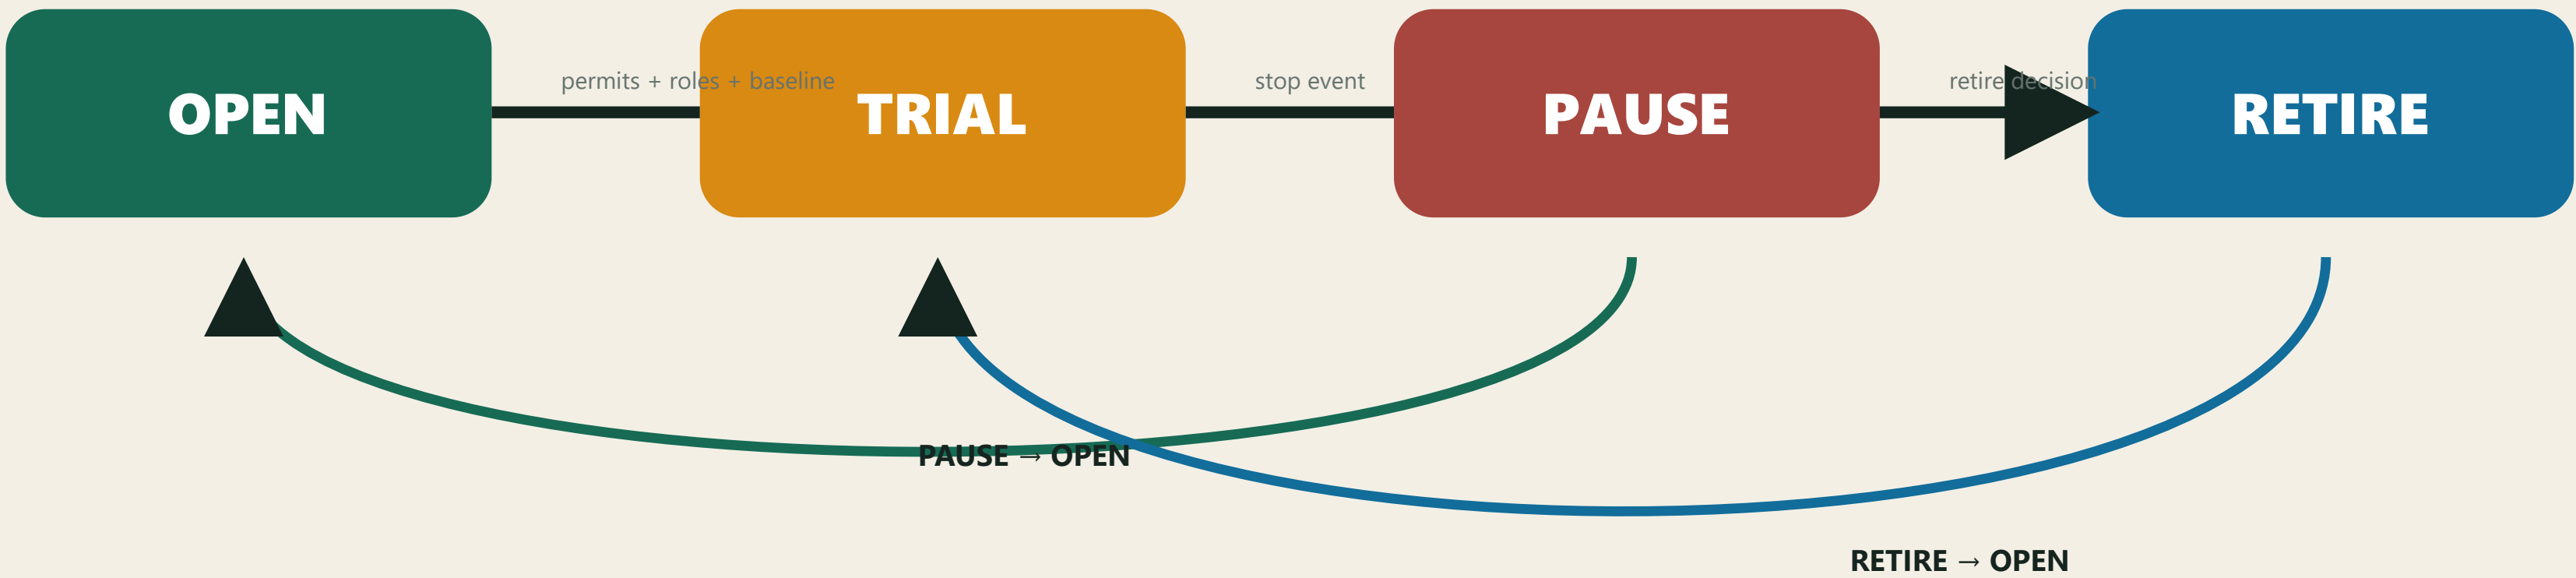

12 × 7 = 84 • DETERMINISTIC DESIGN-CONTRACT MATRIX							
	BASE	PERMIT	ROLE	REGRESS	ZERO	RECOVER	RETIRE
SCN-001	PASS	PASS	PASS	PASS	PASS	PASS	PASS
SCN-002	PASS	PASS	PASS	PASS	PASS	PASS	PASS
SCN-003	PASS	PASS	PASS	PASS	PASS	PASS	PASS
SCN-004	PASS	PASS	PASS	PASS	PASS	PASS	PASS
SCN-005	PASS	PASS	PASS	PASS	PASS	PASS	PASS
SCN-006	PASS	PASS	PASS	PASS	PASS	PASS	PASS
SCN-007	PASS	PASS	PASS	PASS	PASS	PASS	PASS
SCN-008	PASS	PASS	PASS	PASS	PASS	PASS	PASS
SCN-009	PASS	PASS	PASS	PASS	PASS	PASS	PASS
SCN-010	PASS	PASS	PASS	PASS	PASS	PASS	PASS
SCN-011	PASS	PASS	PASS	PASS	PASS	PASS	PASS
SCN-012	PASS	PASS	PASS	PASS	PASS	PASS	PASS
84 / 84 PASS • INPUT HASHED • RULE VERSIONED • FIELD RESULT COUNT = 0							

synthetic_design_verification verifies only design-state, admission, stop, recovery and retirement rules; not field safety, transport efficiency, public acceptance or approval.

SYNTHETIC RECEIPT EXAMPLE

SCN-010-T05 • ZERO-TOLERANCE EVENT

INITIAL

TRIAL

EVENT

zero_tolerance_event_detected

EXPECTED / OBSERVED

PAUSE / PAUSE

ACCOUNTABLE TRIGGER


safety lead stops immediately

RECOVERY EXIT

staffed task + route restoration

KNOWN DESIGN	geometry, quantity, documents
SYNTHETIC	rule consistency, not performance
FIELD UNKNOWN	safety, efficiency, acceptance, cost

ONE OPERATING DAY • SIX STEPS CONNECT SPACE, OWNER + EXIT

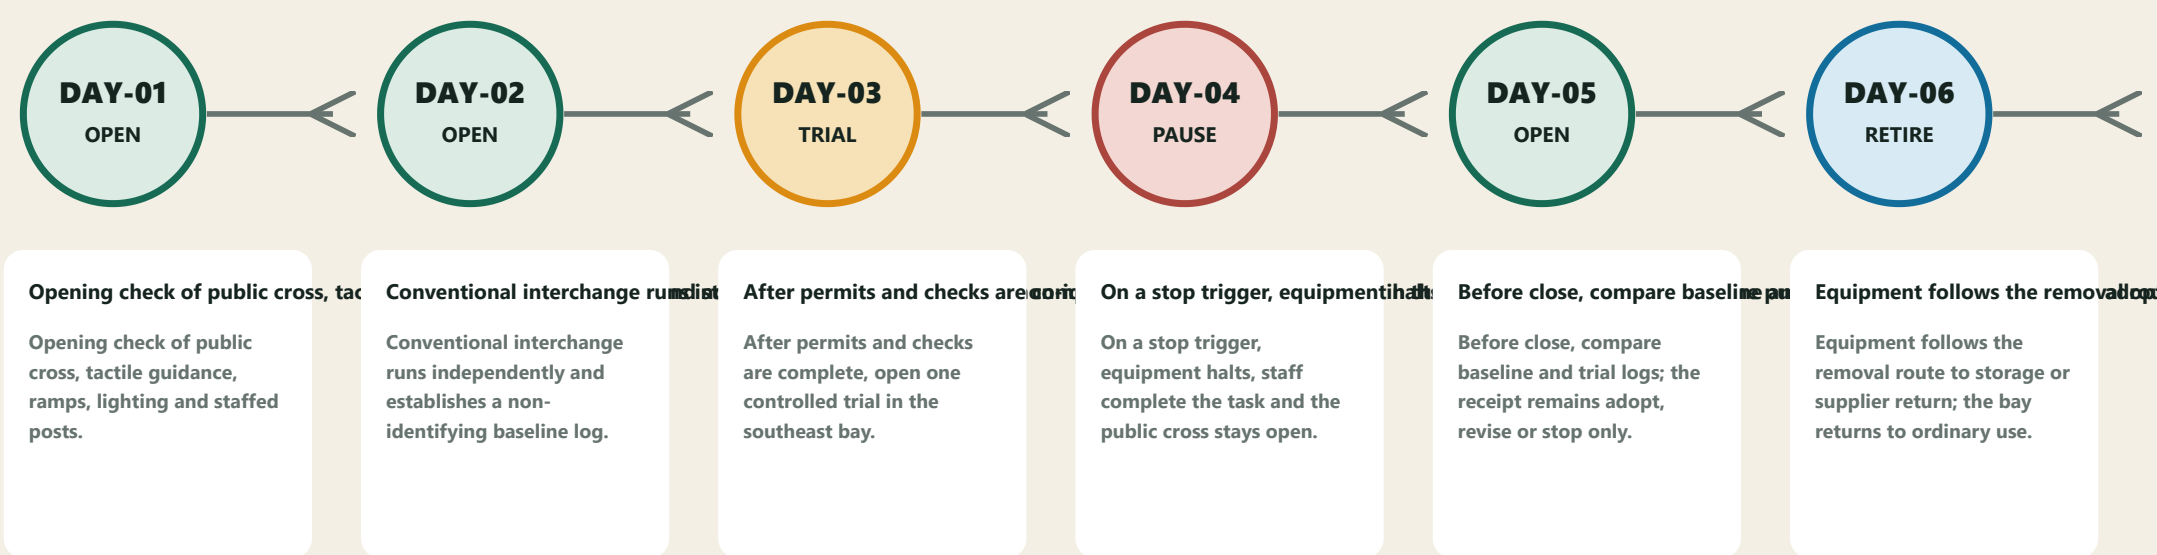

RECOVERY CLOCK: stop command – staff complete baseline – both public routes open
No target before E2 drill; formal quote, field performance and adoption remain pending.

90-DAY ENTRY GATES

00–30
baseline only

31–45
field baseline

46–75
permitted trial

76–90
stop, retire, receipt

ADOPT • REVISE • STOP

any failed gate returns to baseline