



重点区域

三处重点区域详细设计（规划综合实施方案深度概念）


众智园AI自主创新加速区

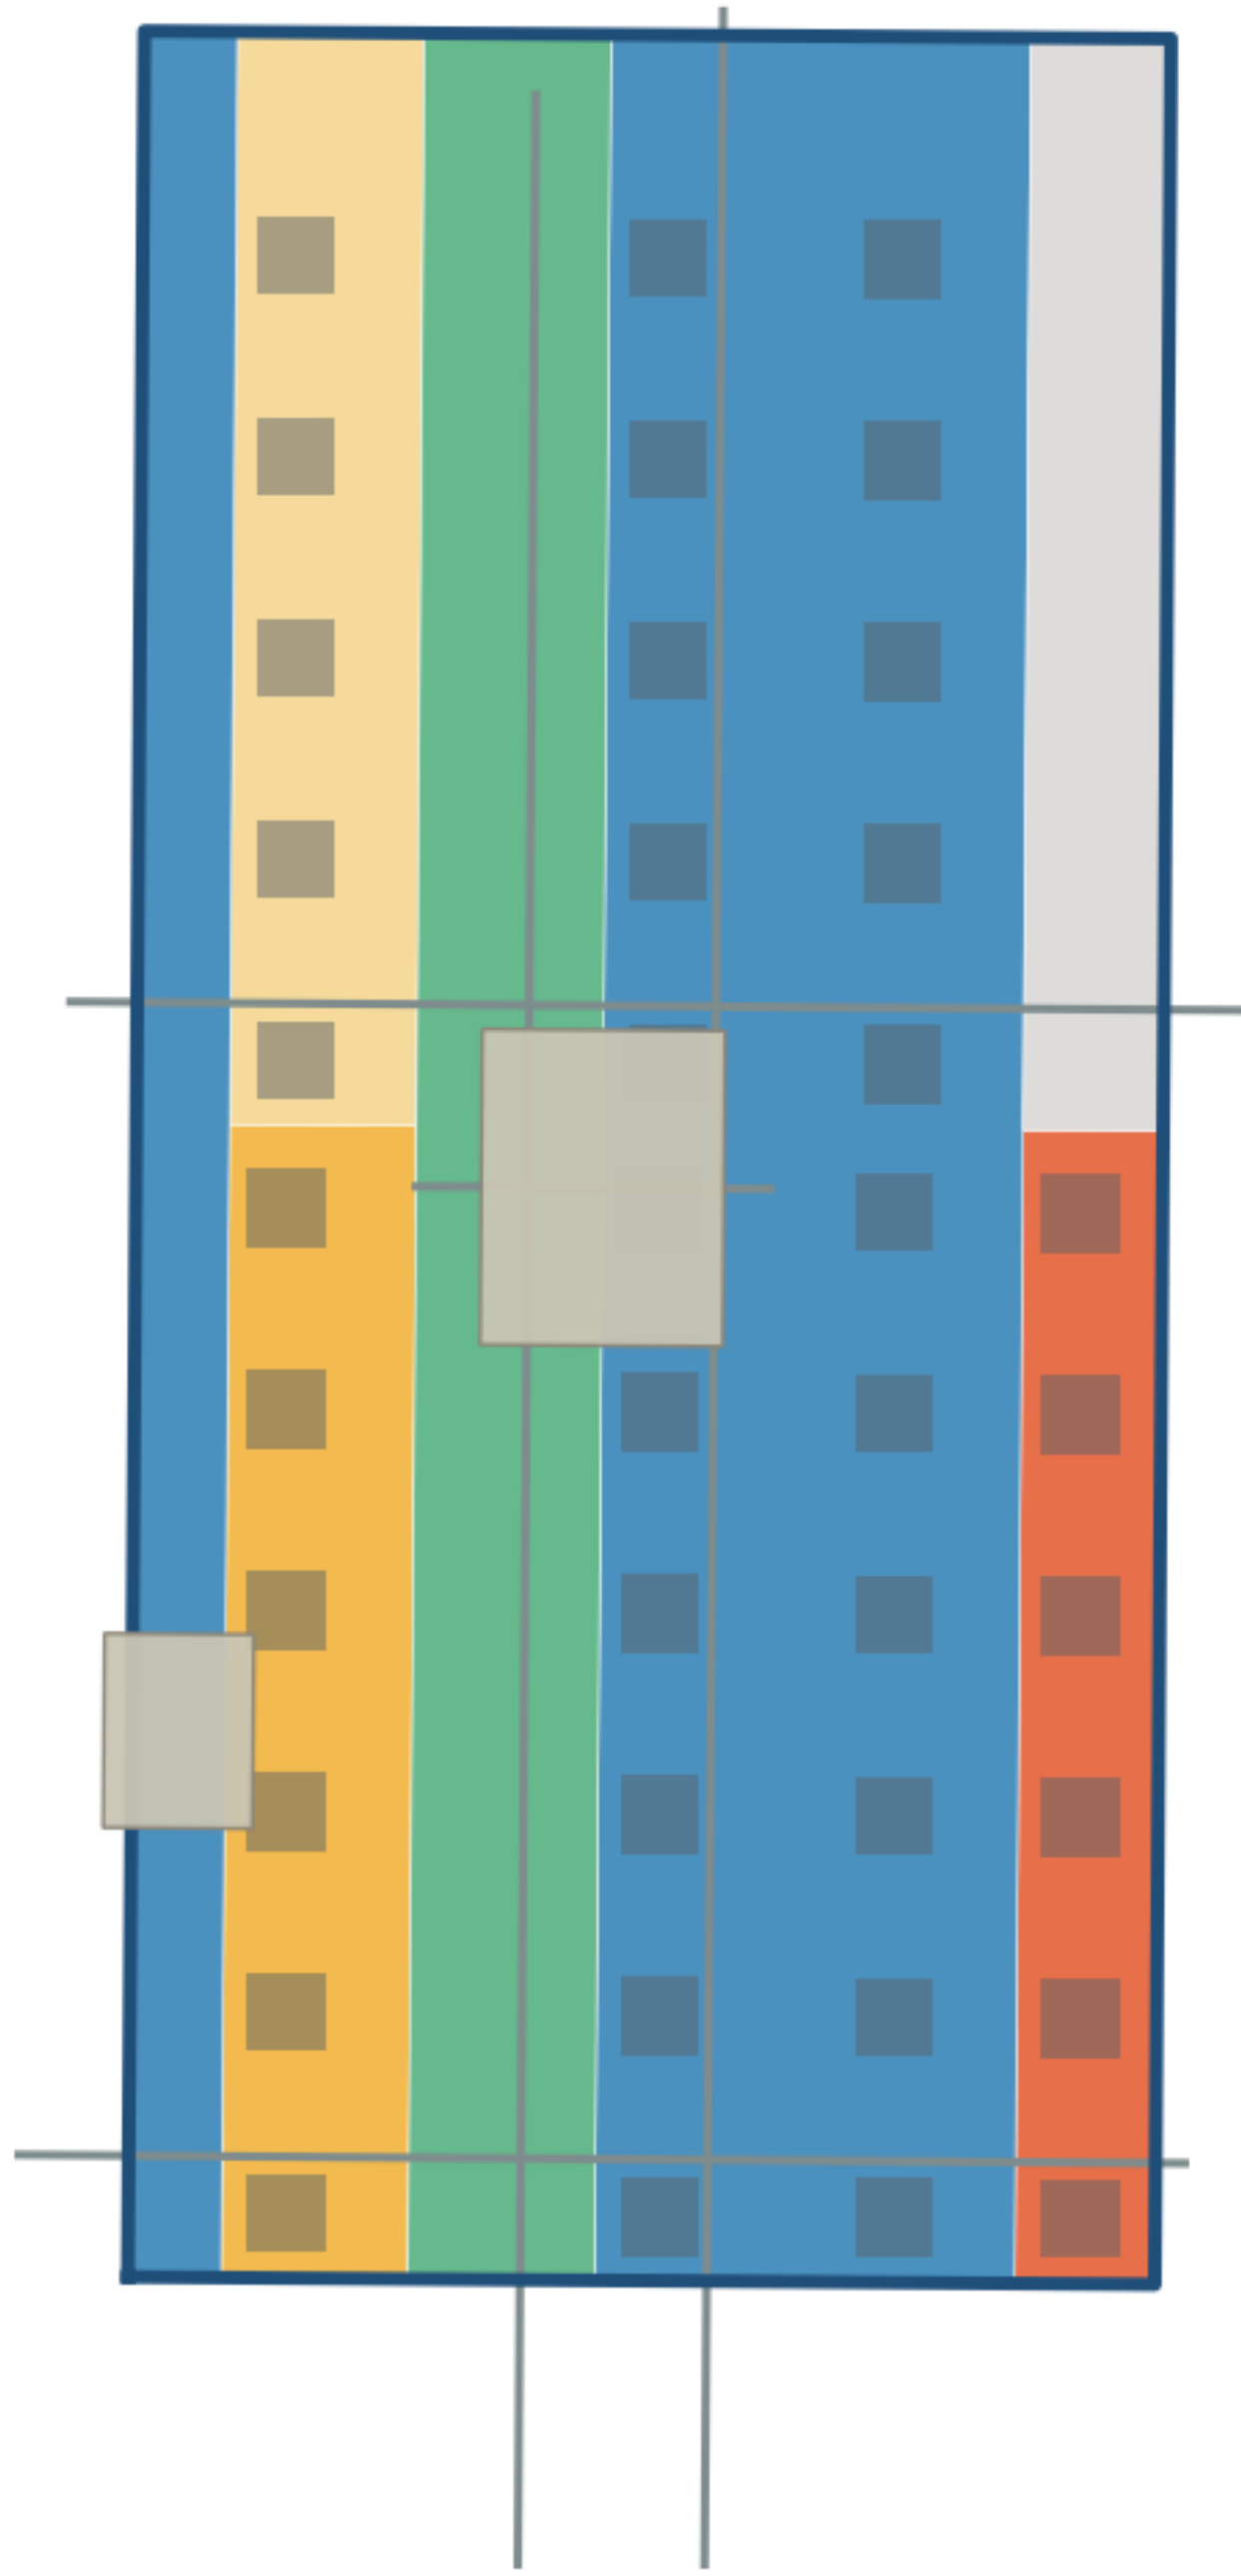

北京AI原点社区

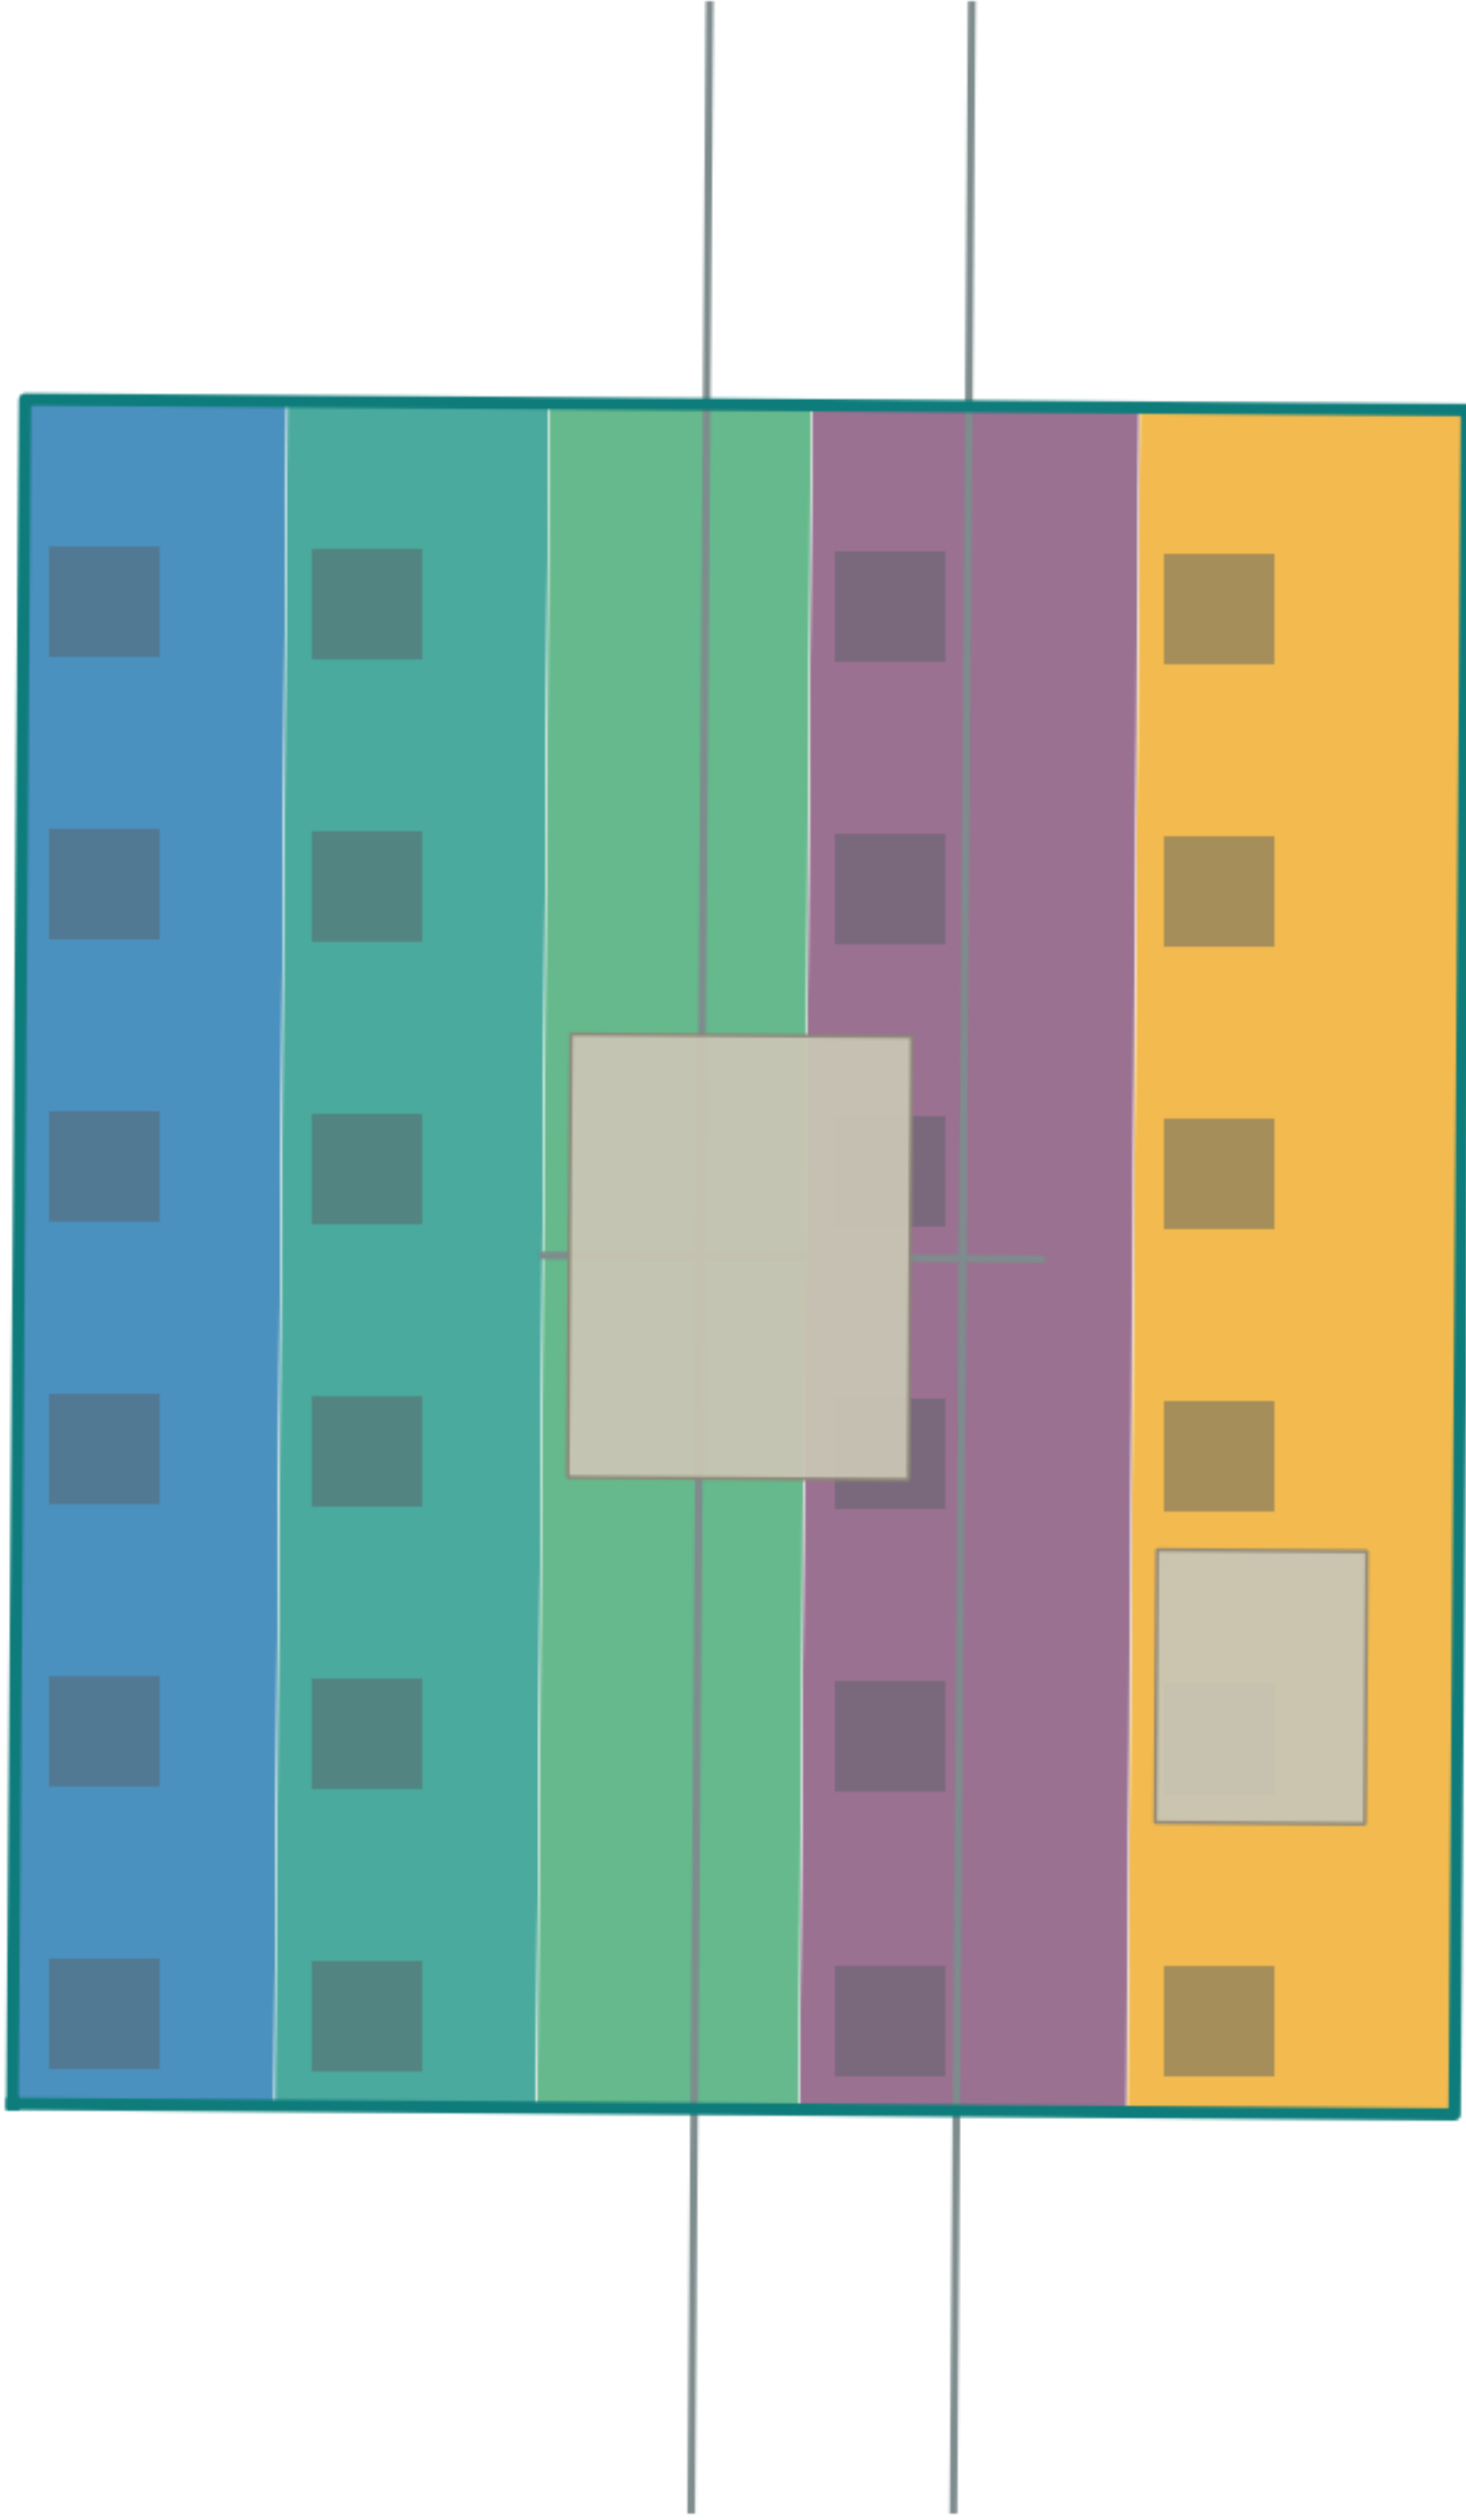


大钟寺AI产业集聚区

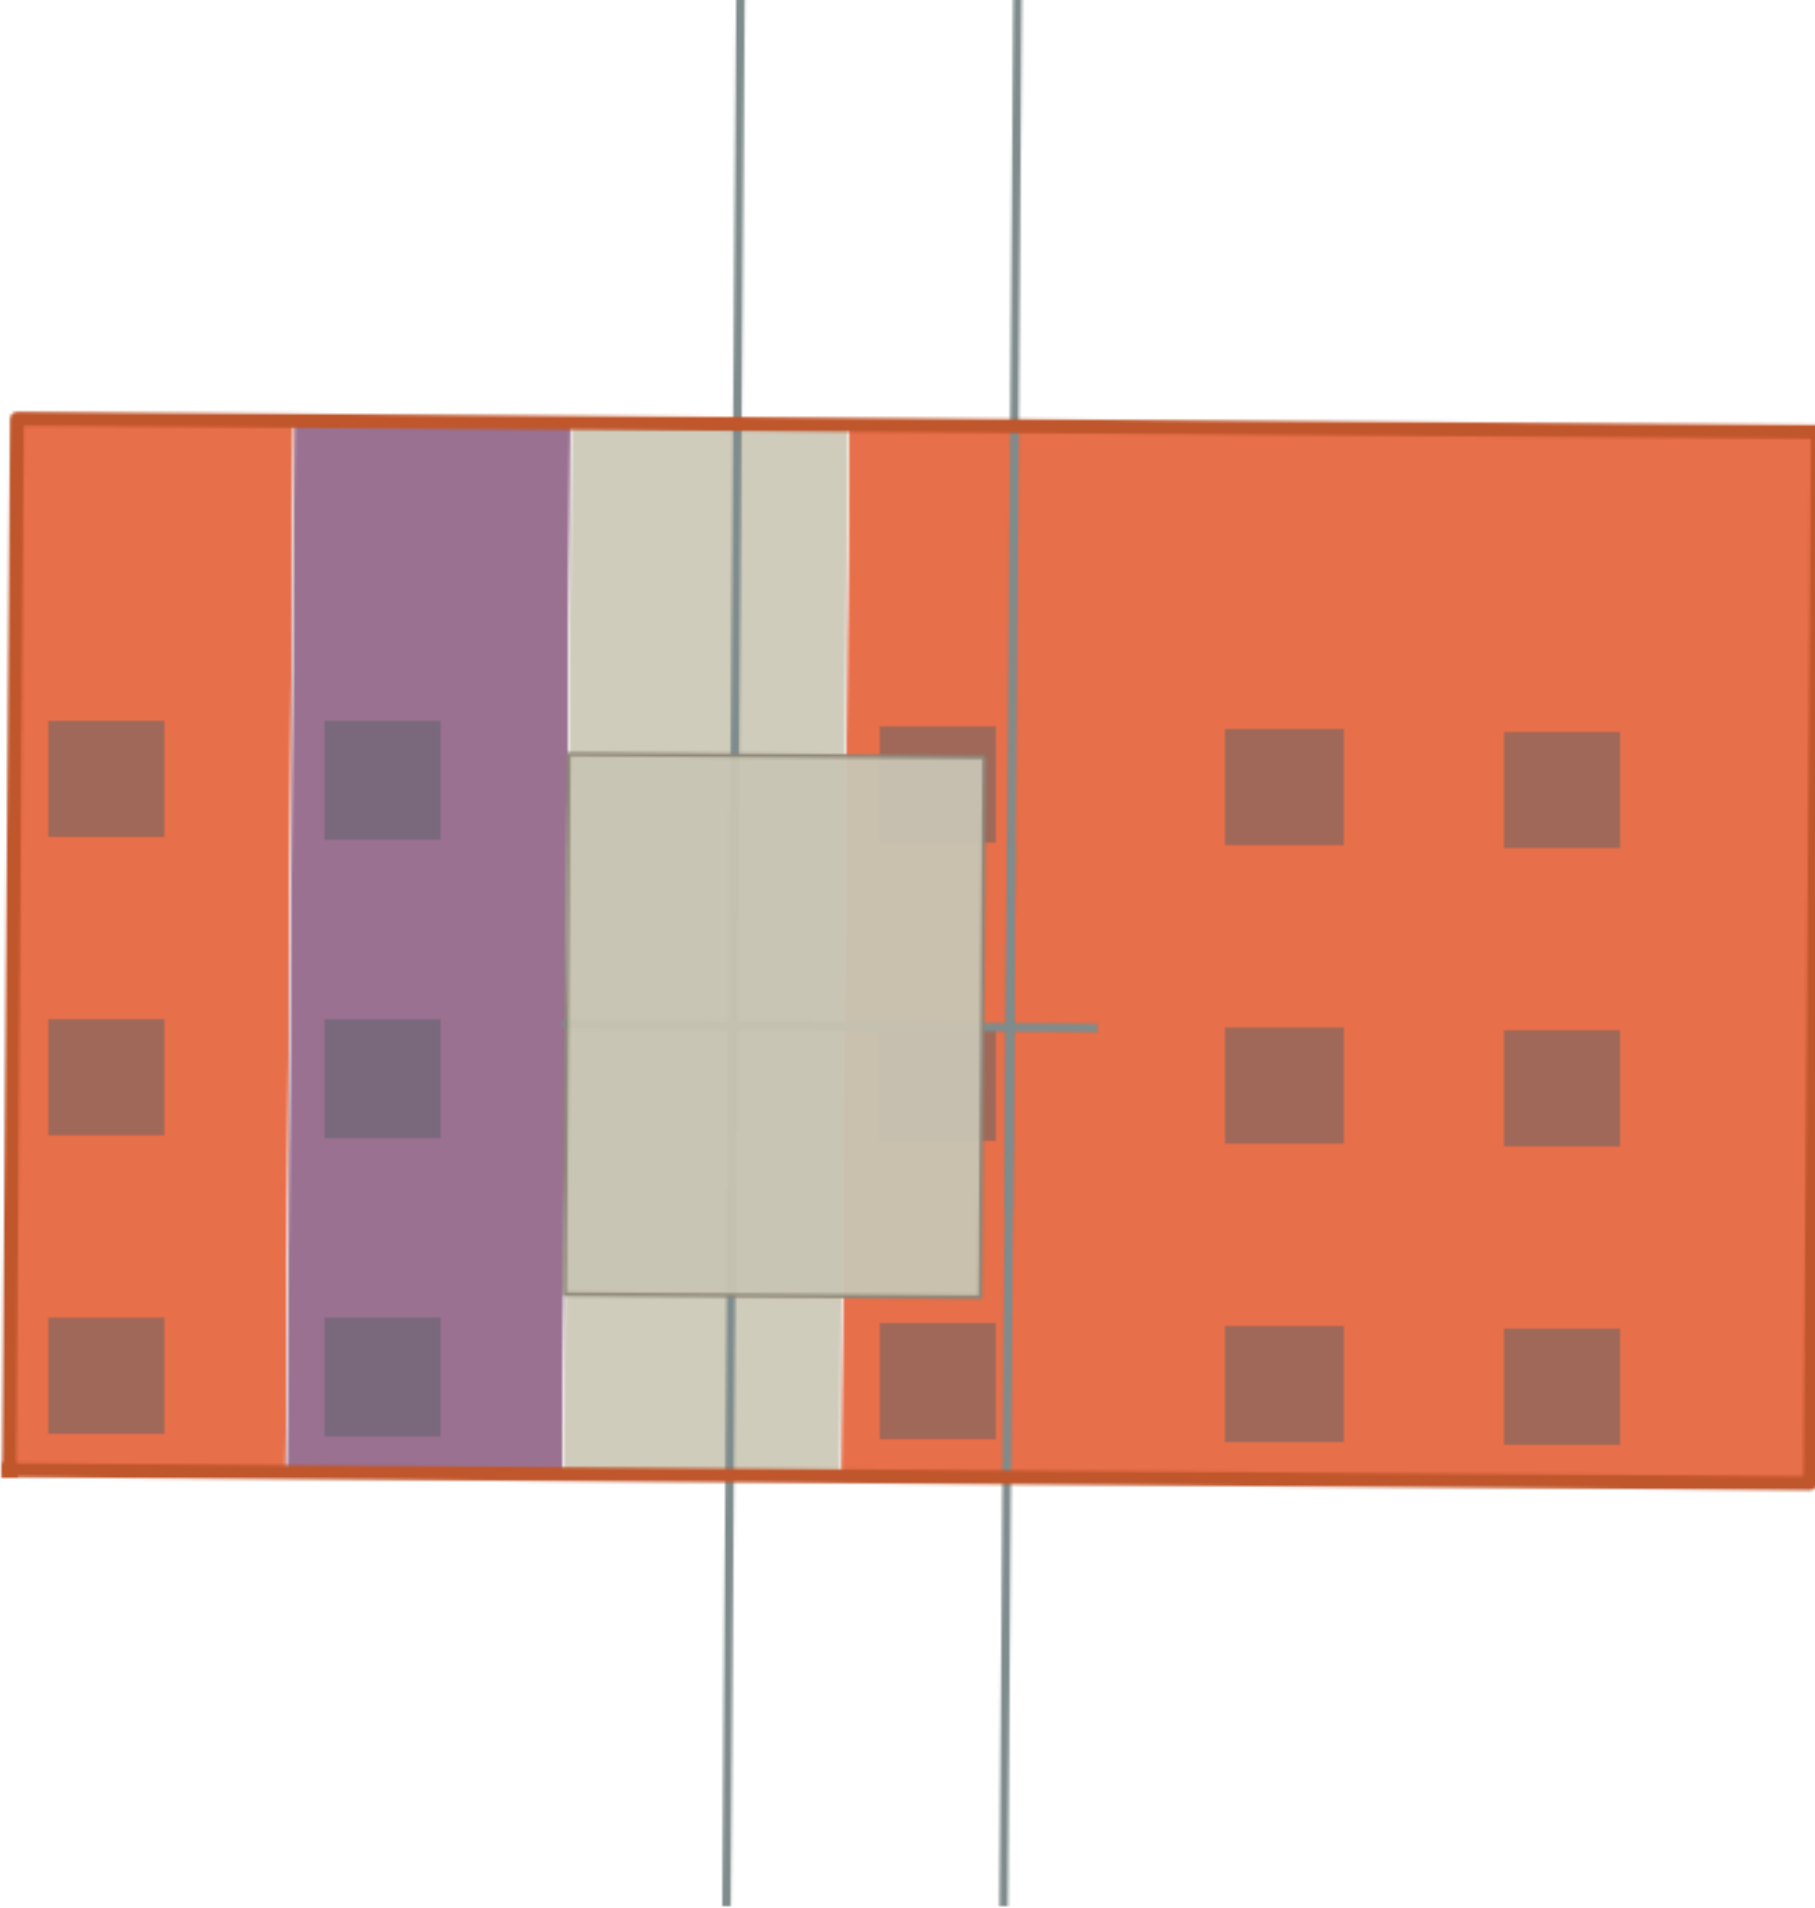



总体设计范围用地结构（控规深度城市设计概念）

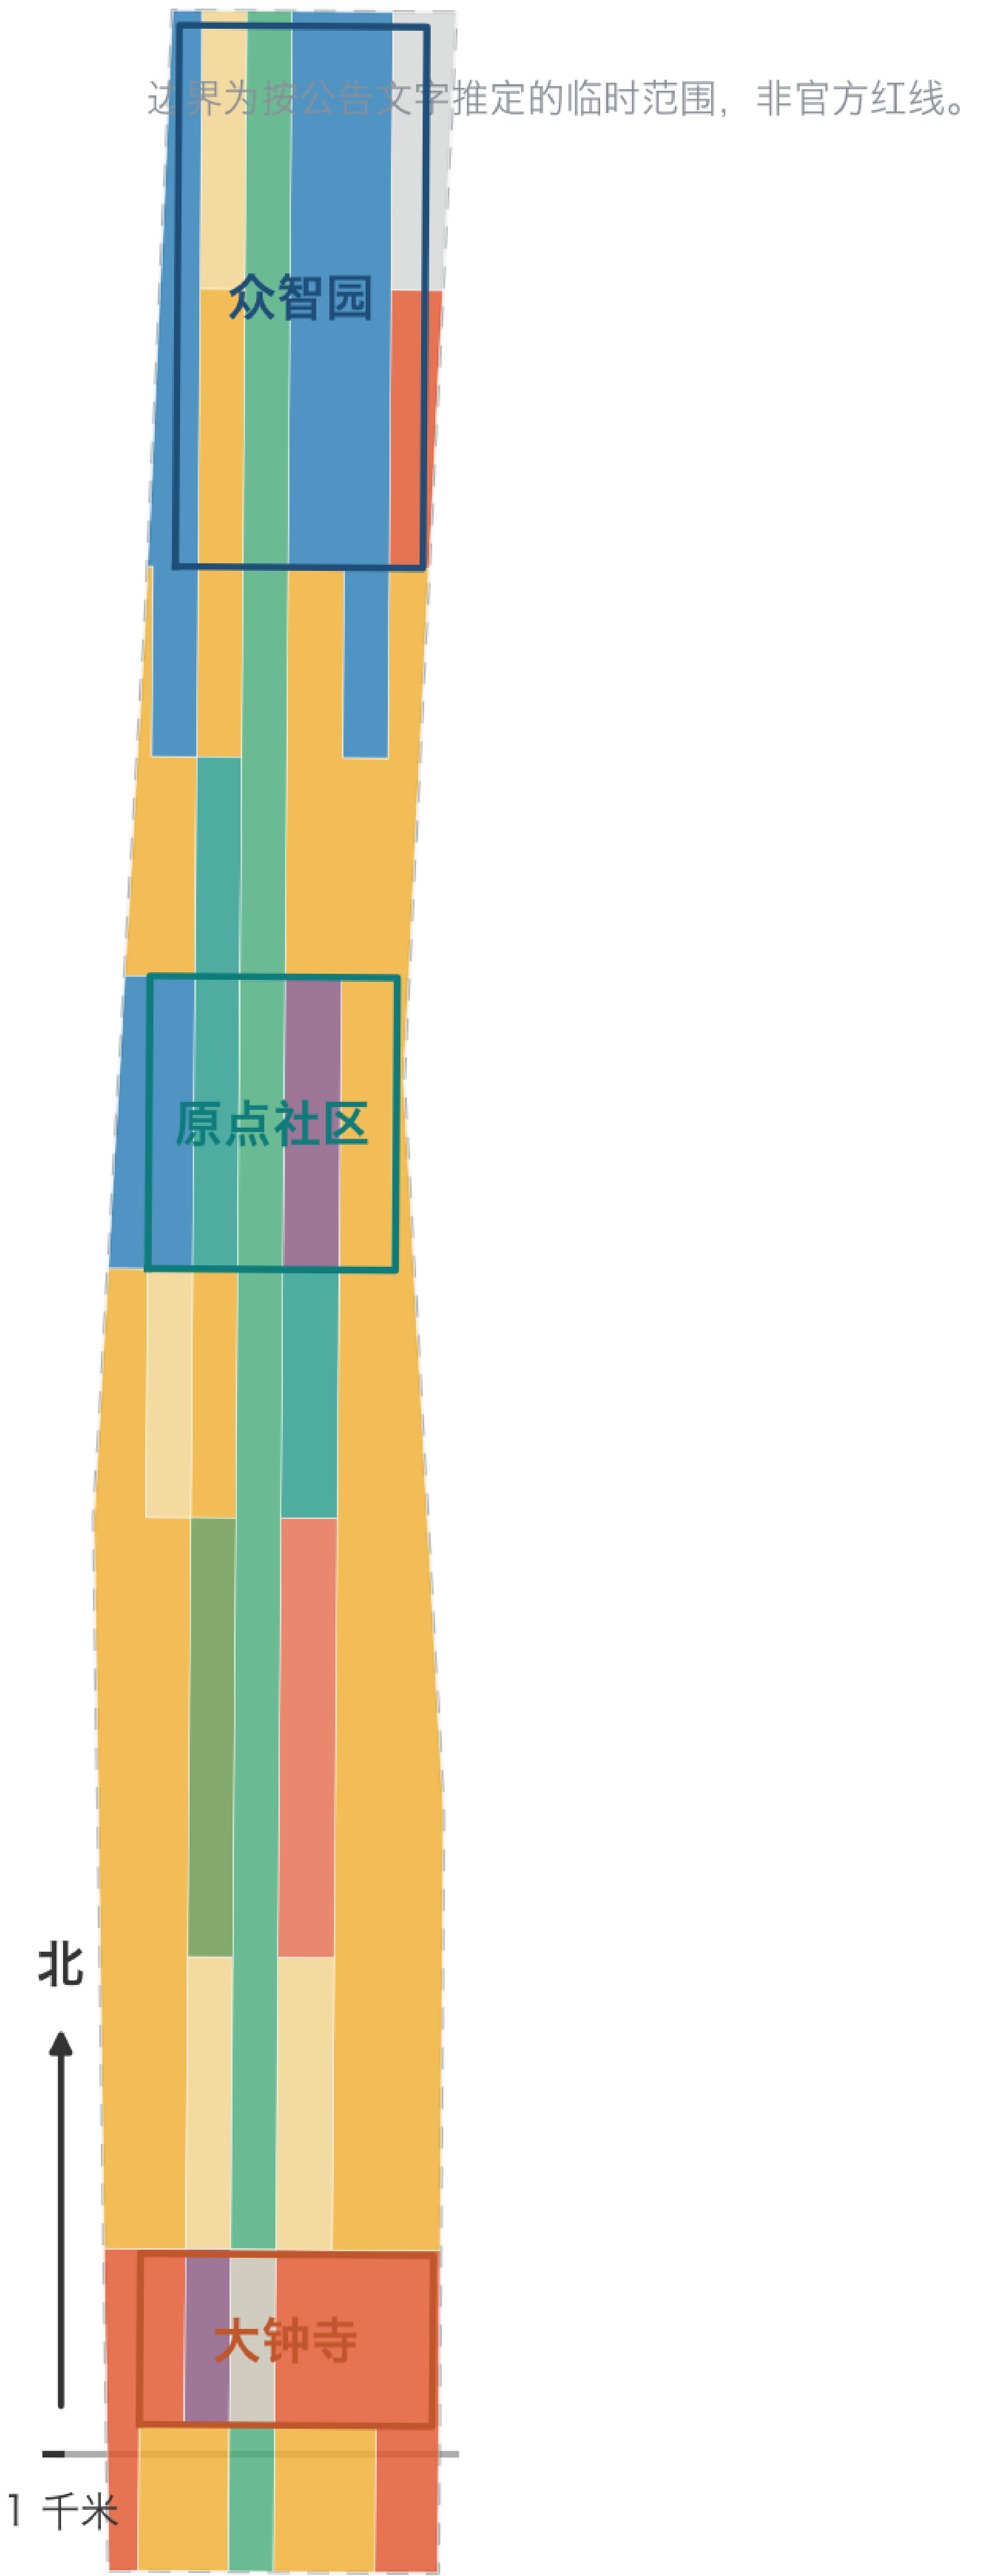

用地分类图例


- 0802 科研用地
- 05 商业服务业用地
- 0701 城镇住宅用地
- 0702 社区服务设施用地
- 0803 文化用地
- 0804 教育用地
- 0805 体育用地
- 0806 医疗卫生用地
- 1401 公园绿地
- 1403 广场用地
- 16 留白用地

依据《国土空间调查、规划、用途管制用地用海分类指南》子集；面积按 EPSG:4548 复算，详见 metrics.json。




核心指标复算与证据链（源自 geometry / metrics.json）


总体设计范围用地分布

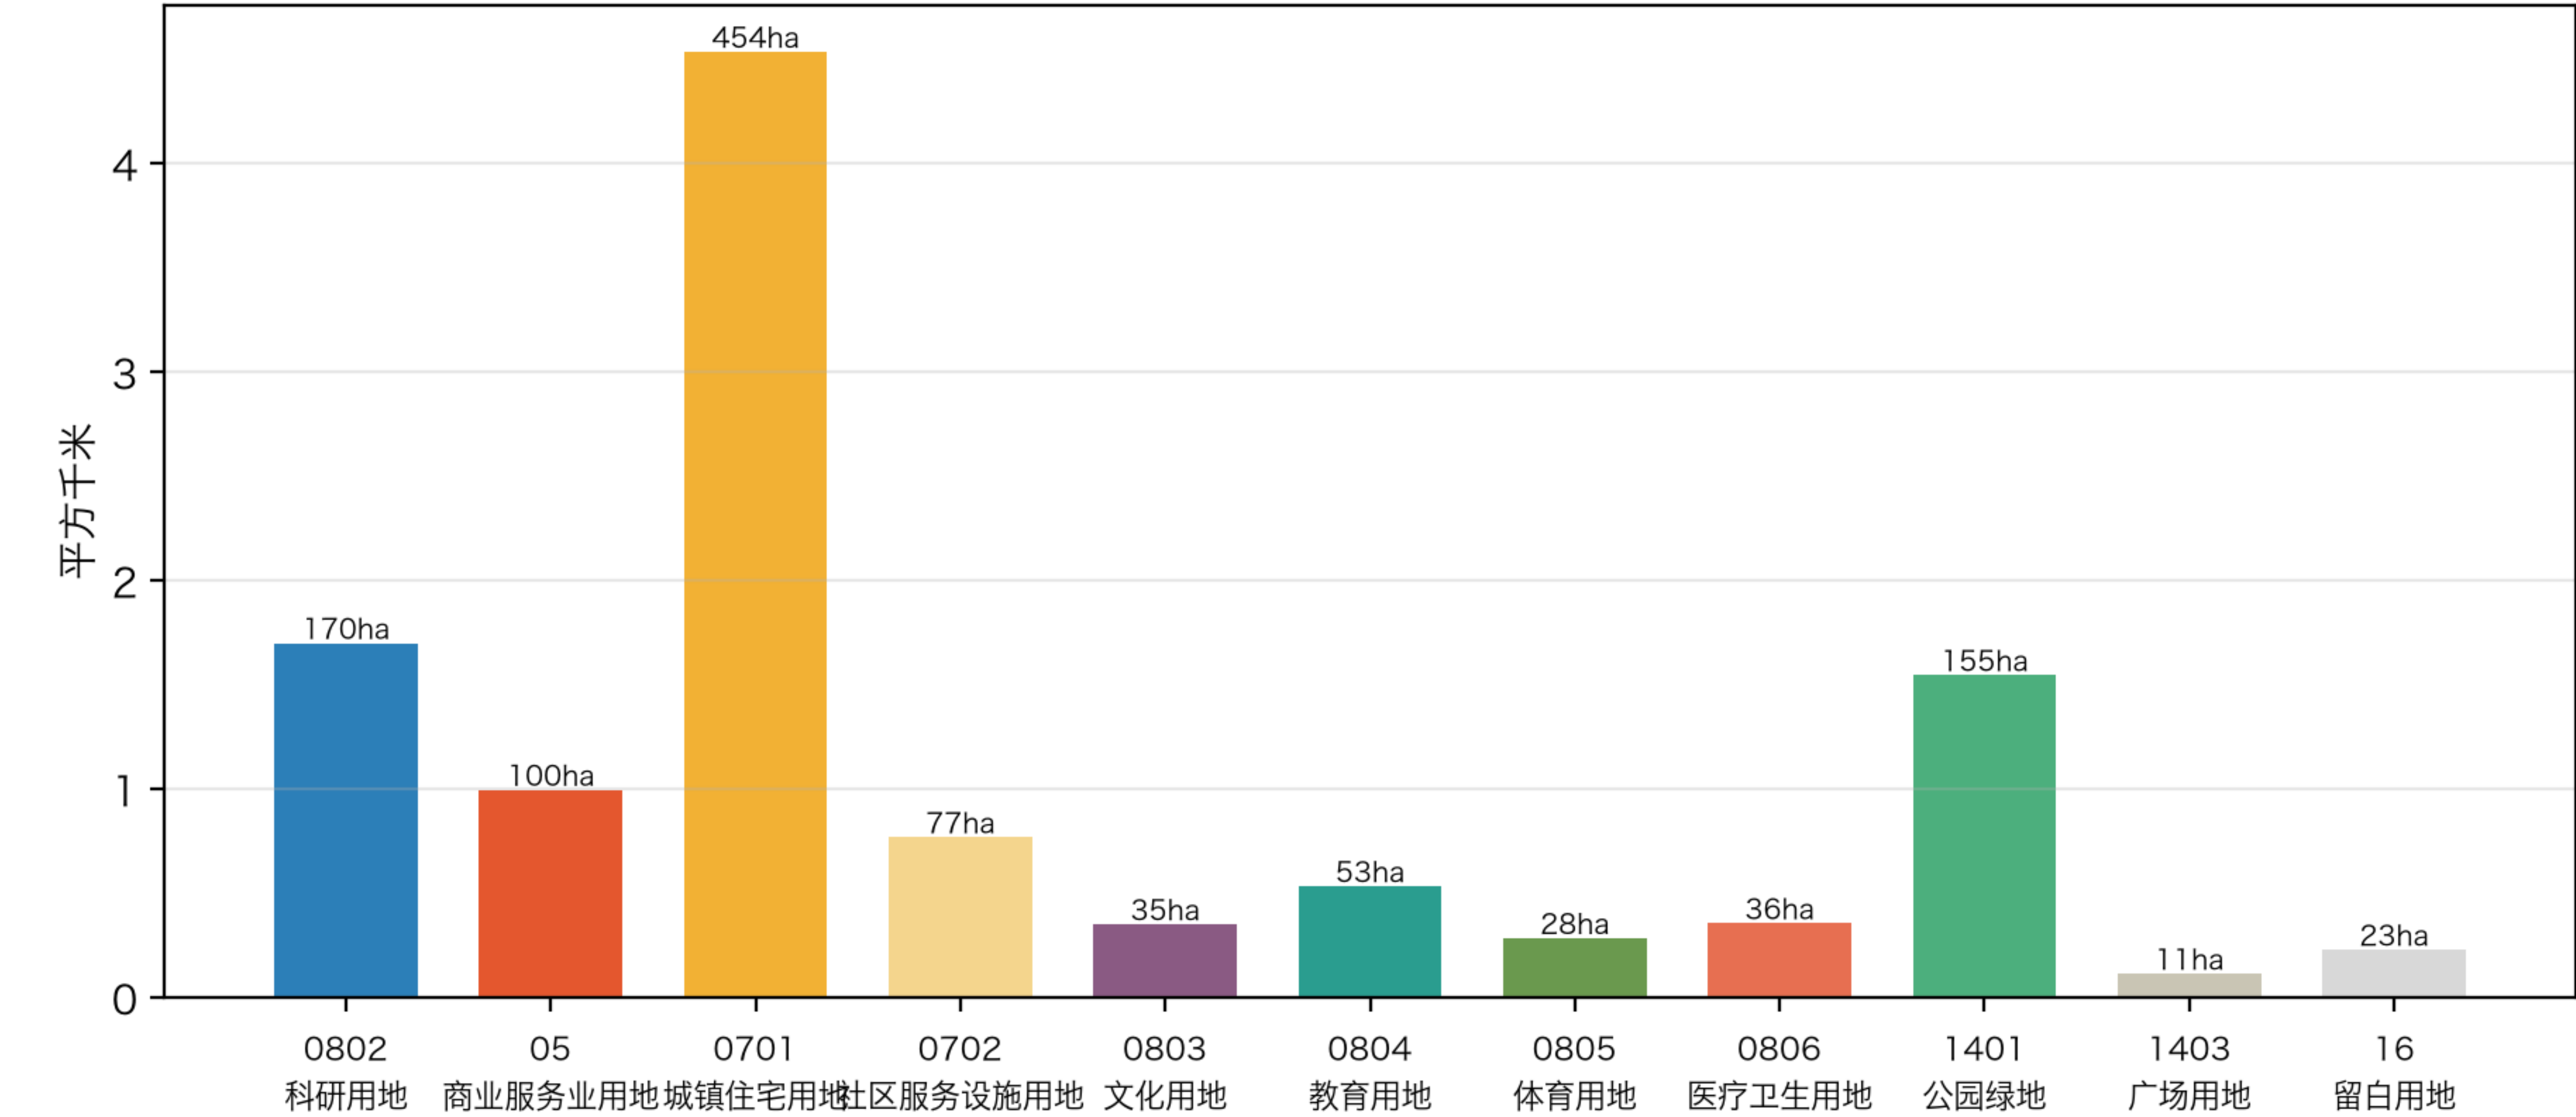


核心空间比例指标

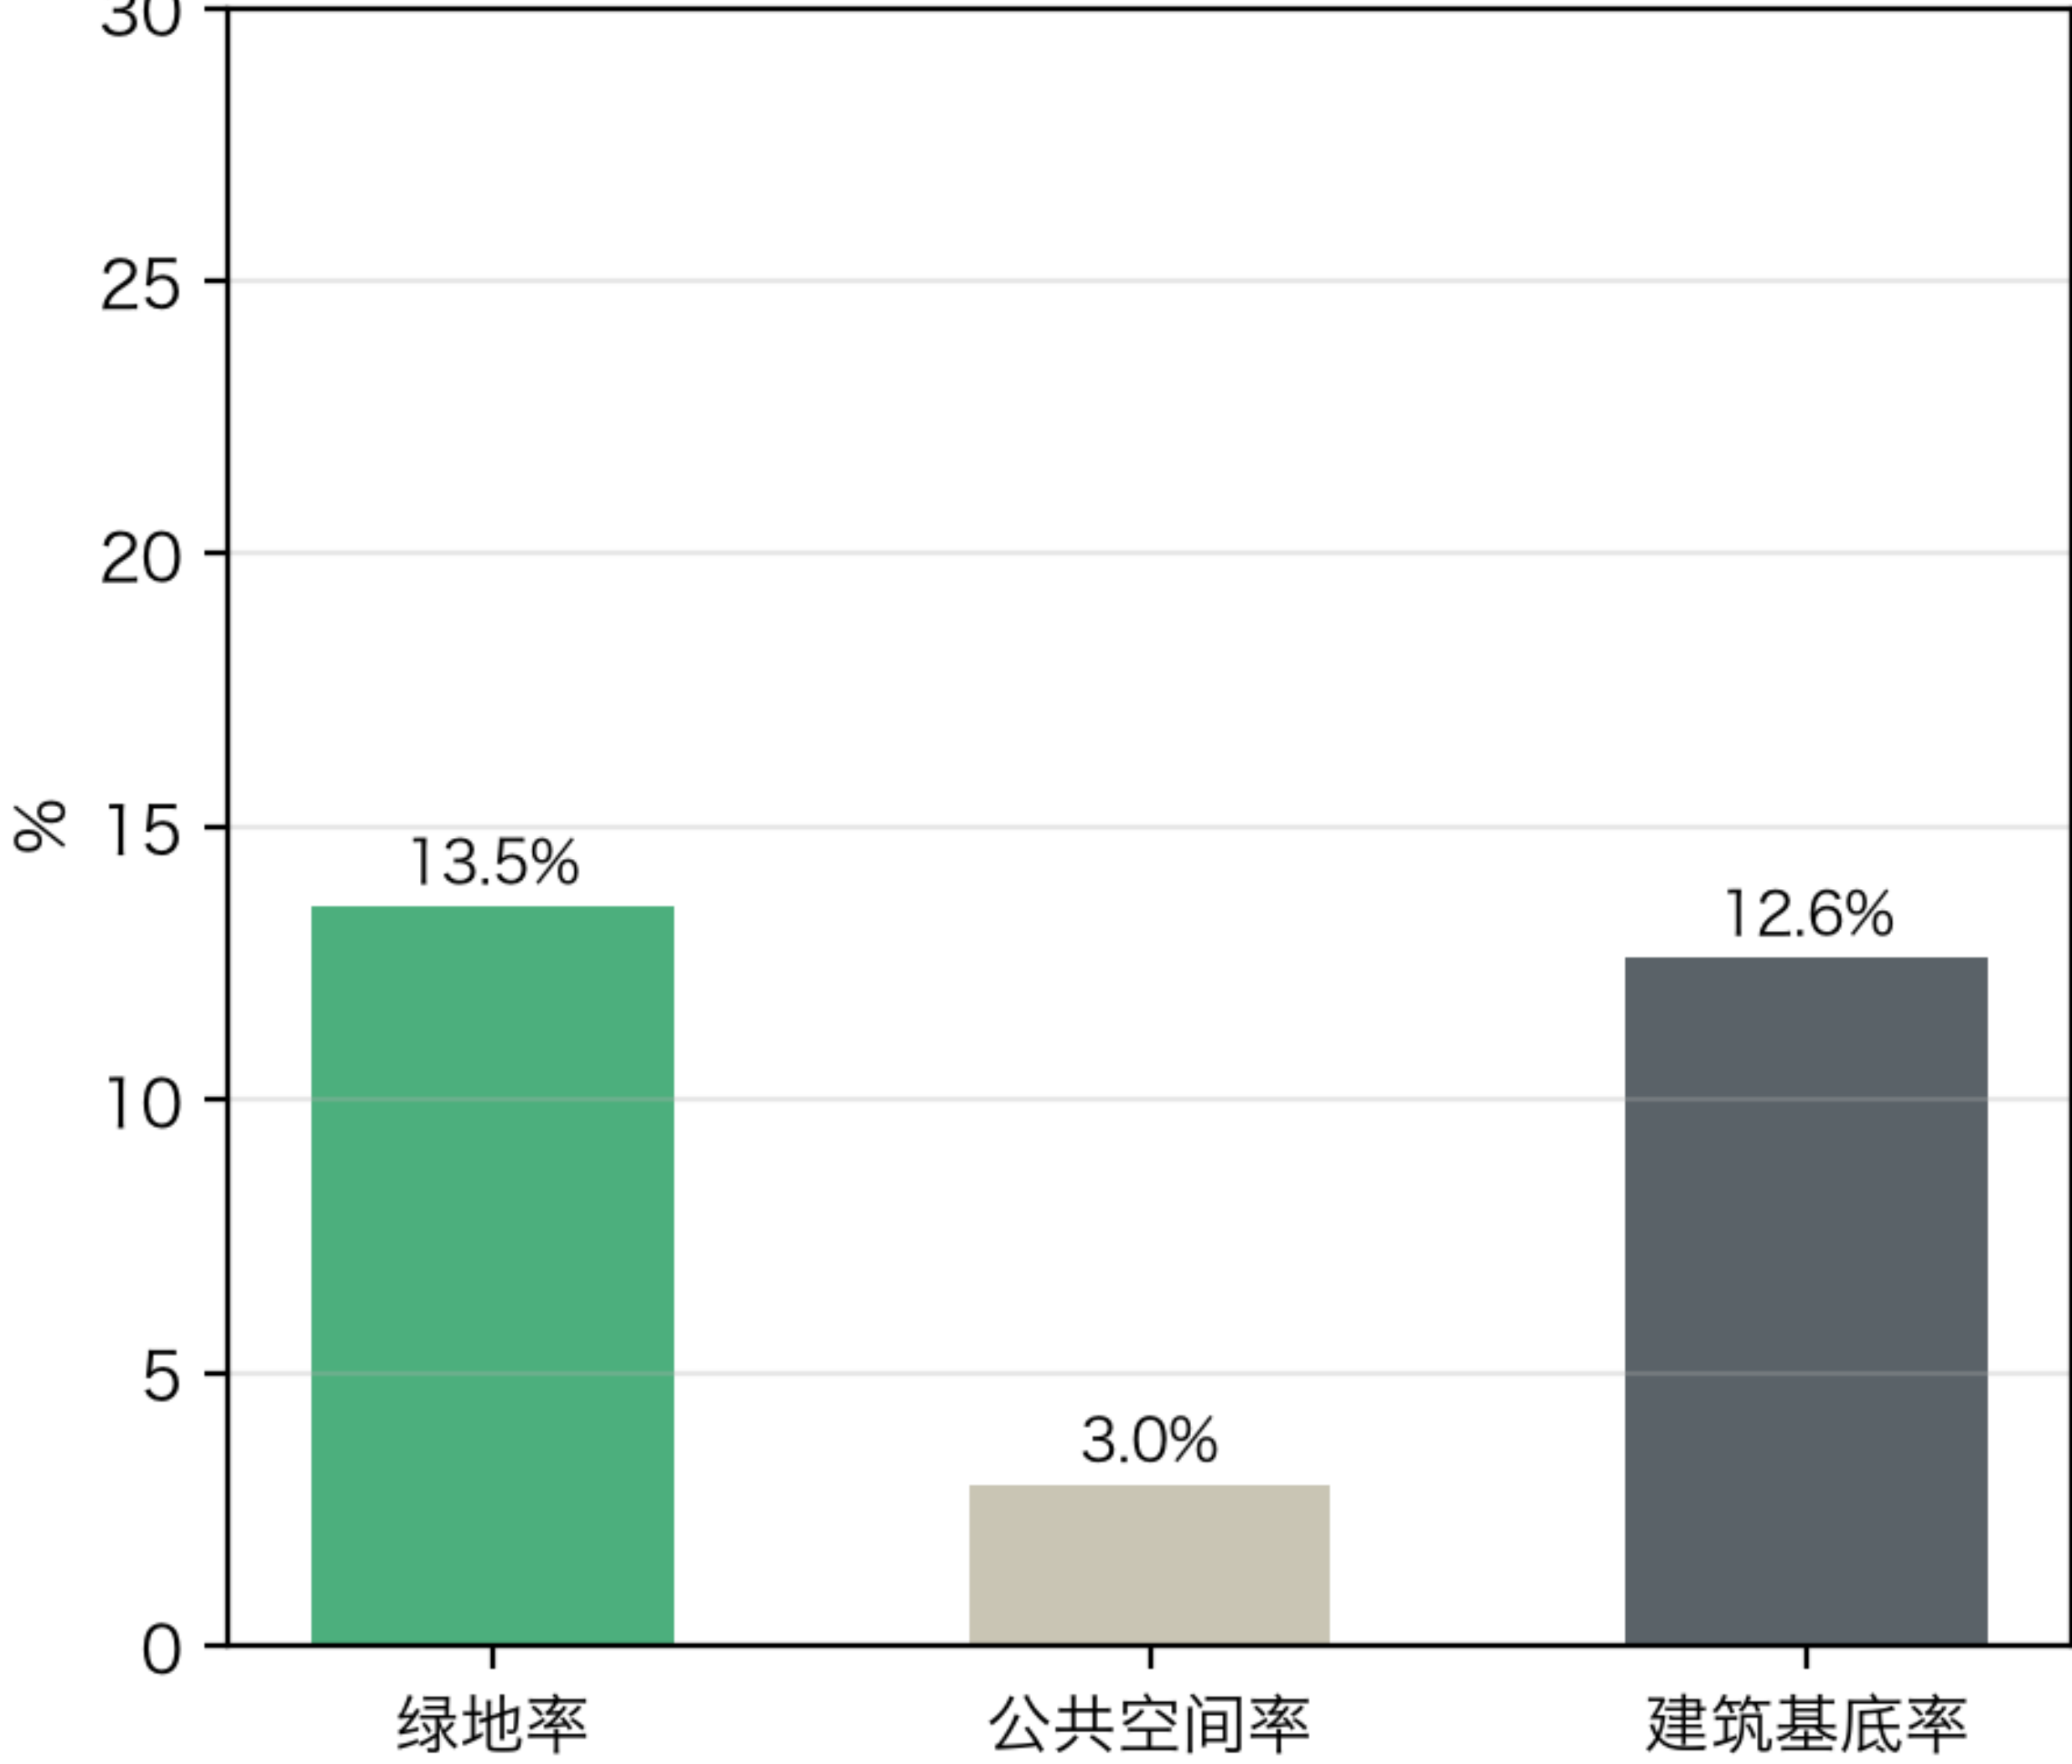

三处重点区域面积

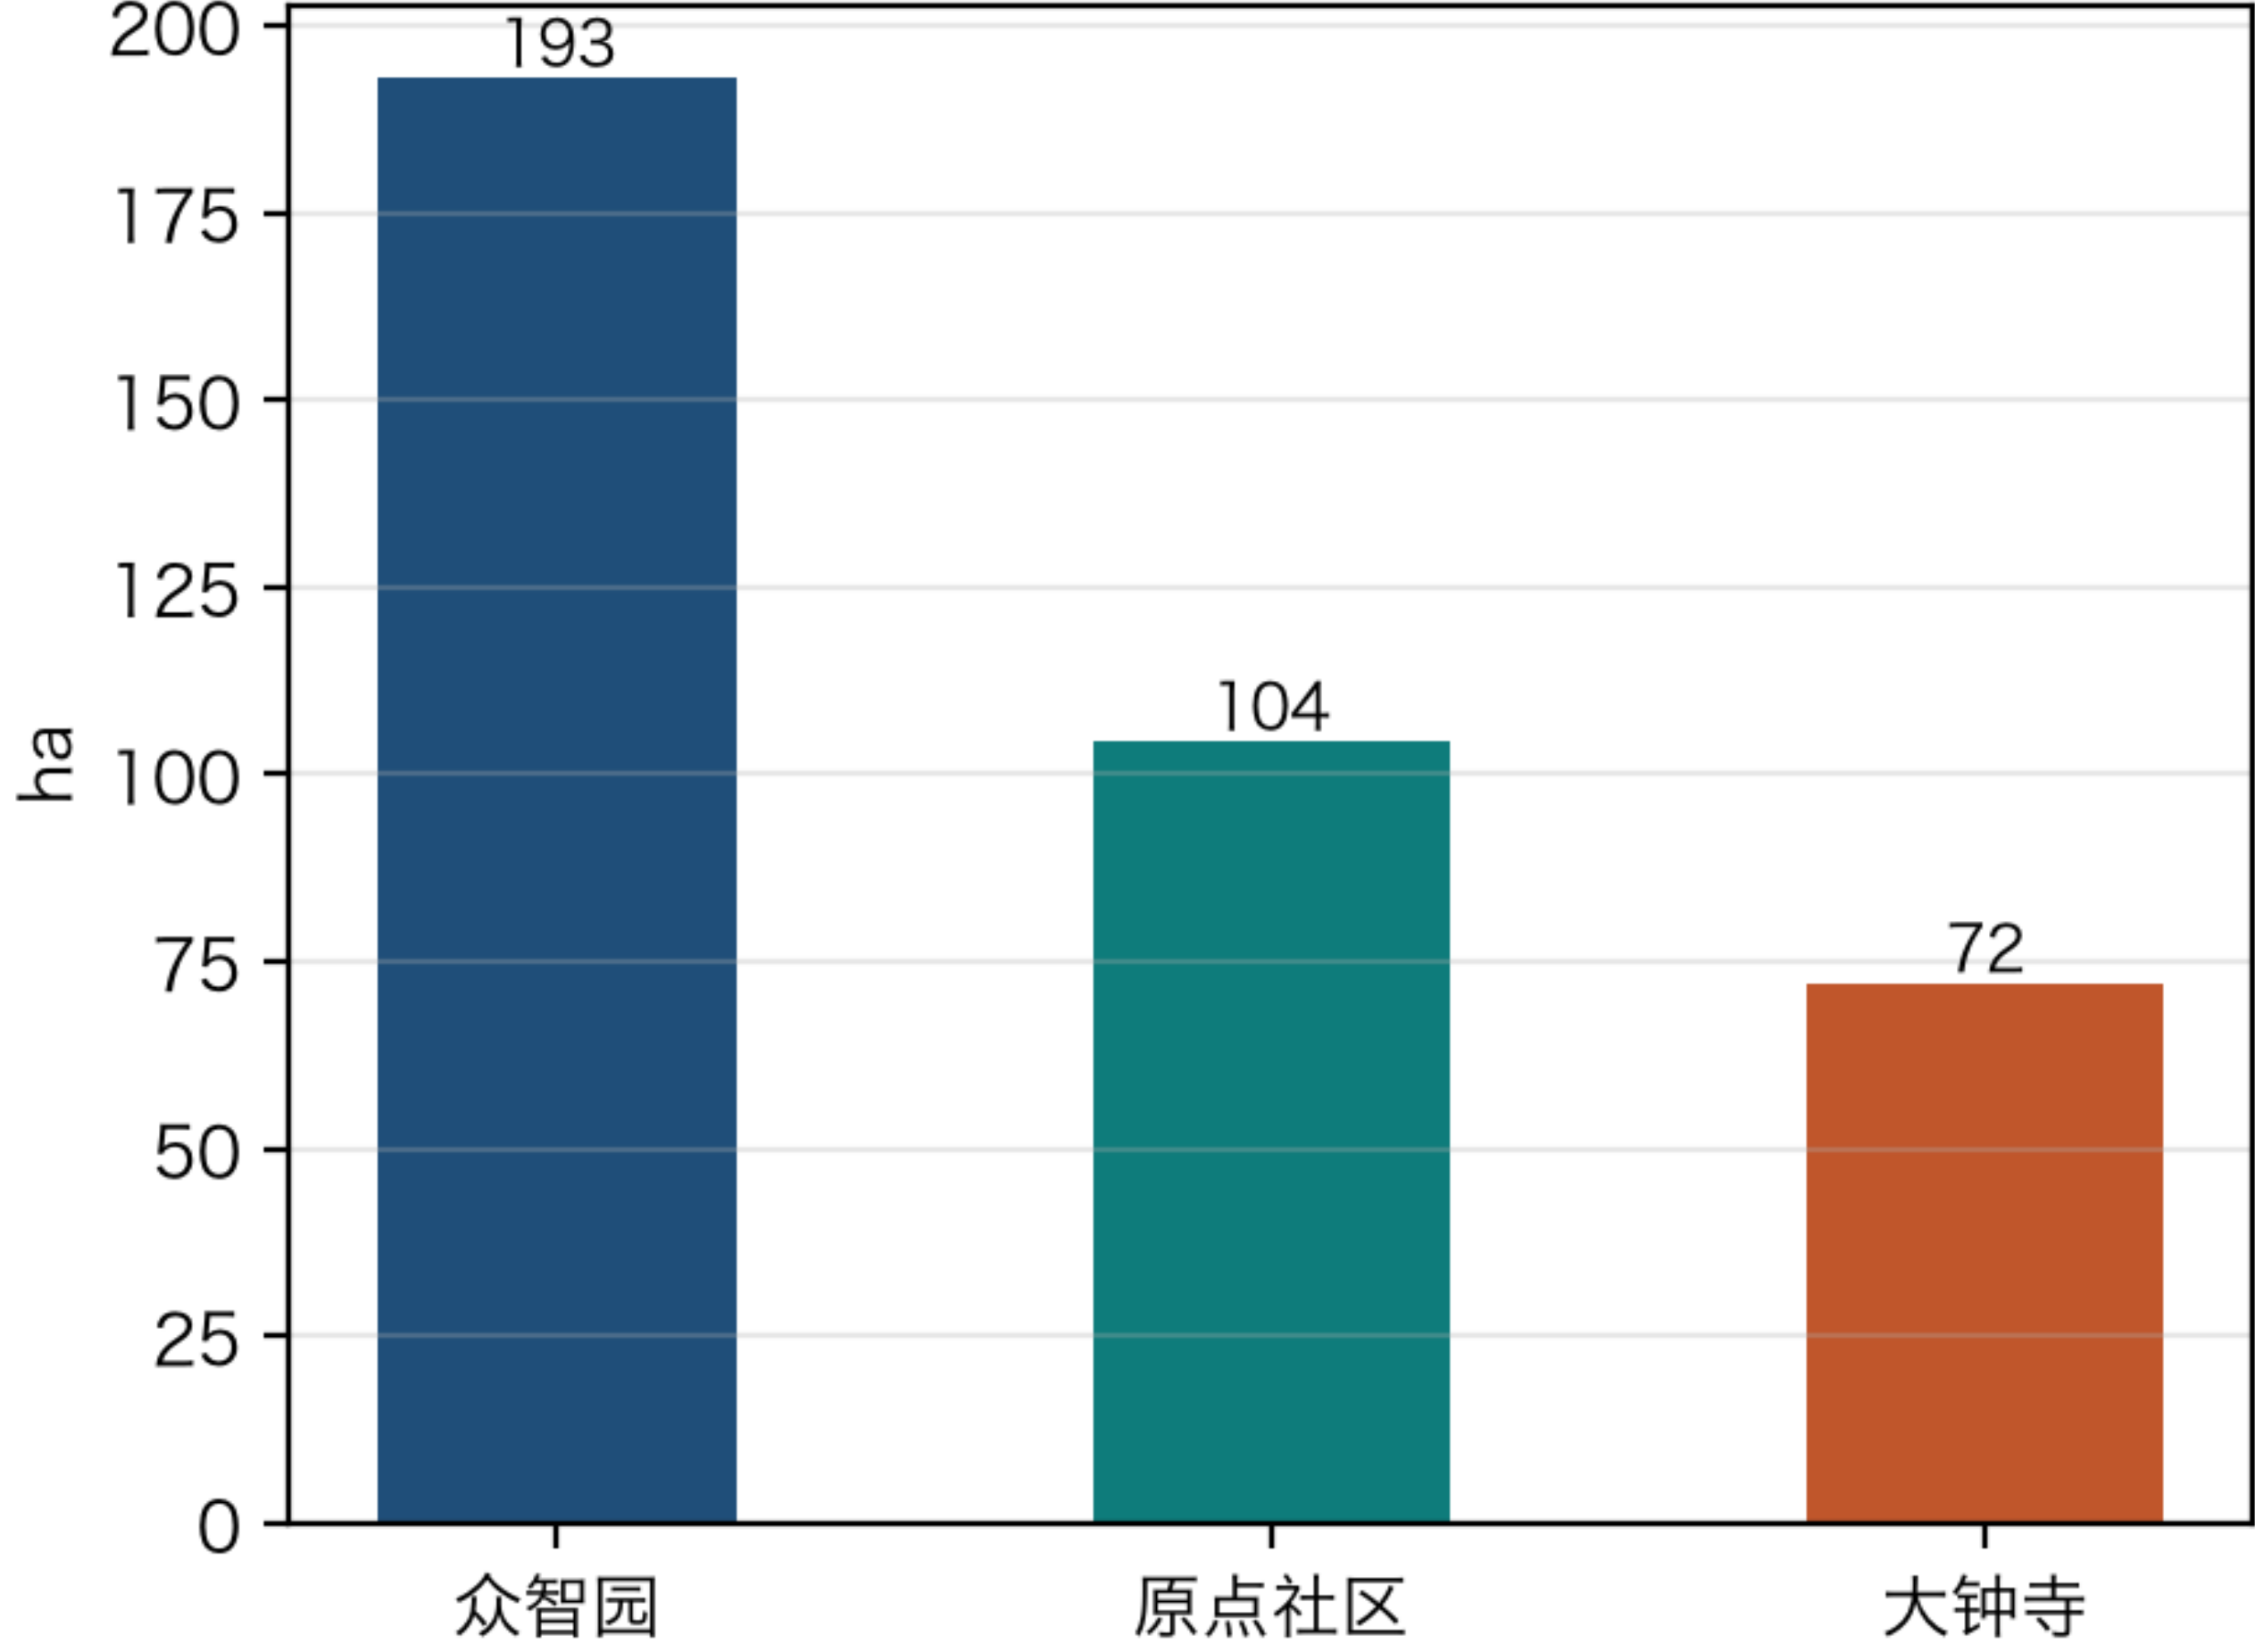

总量与构成

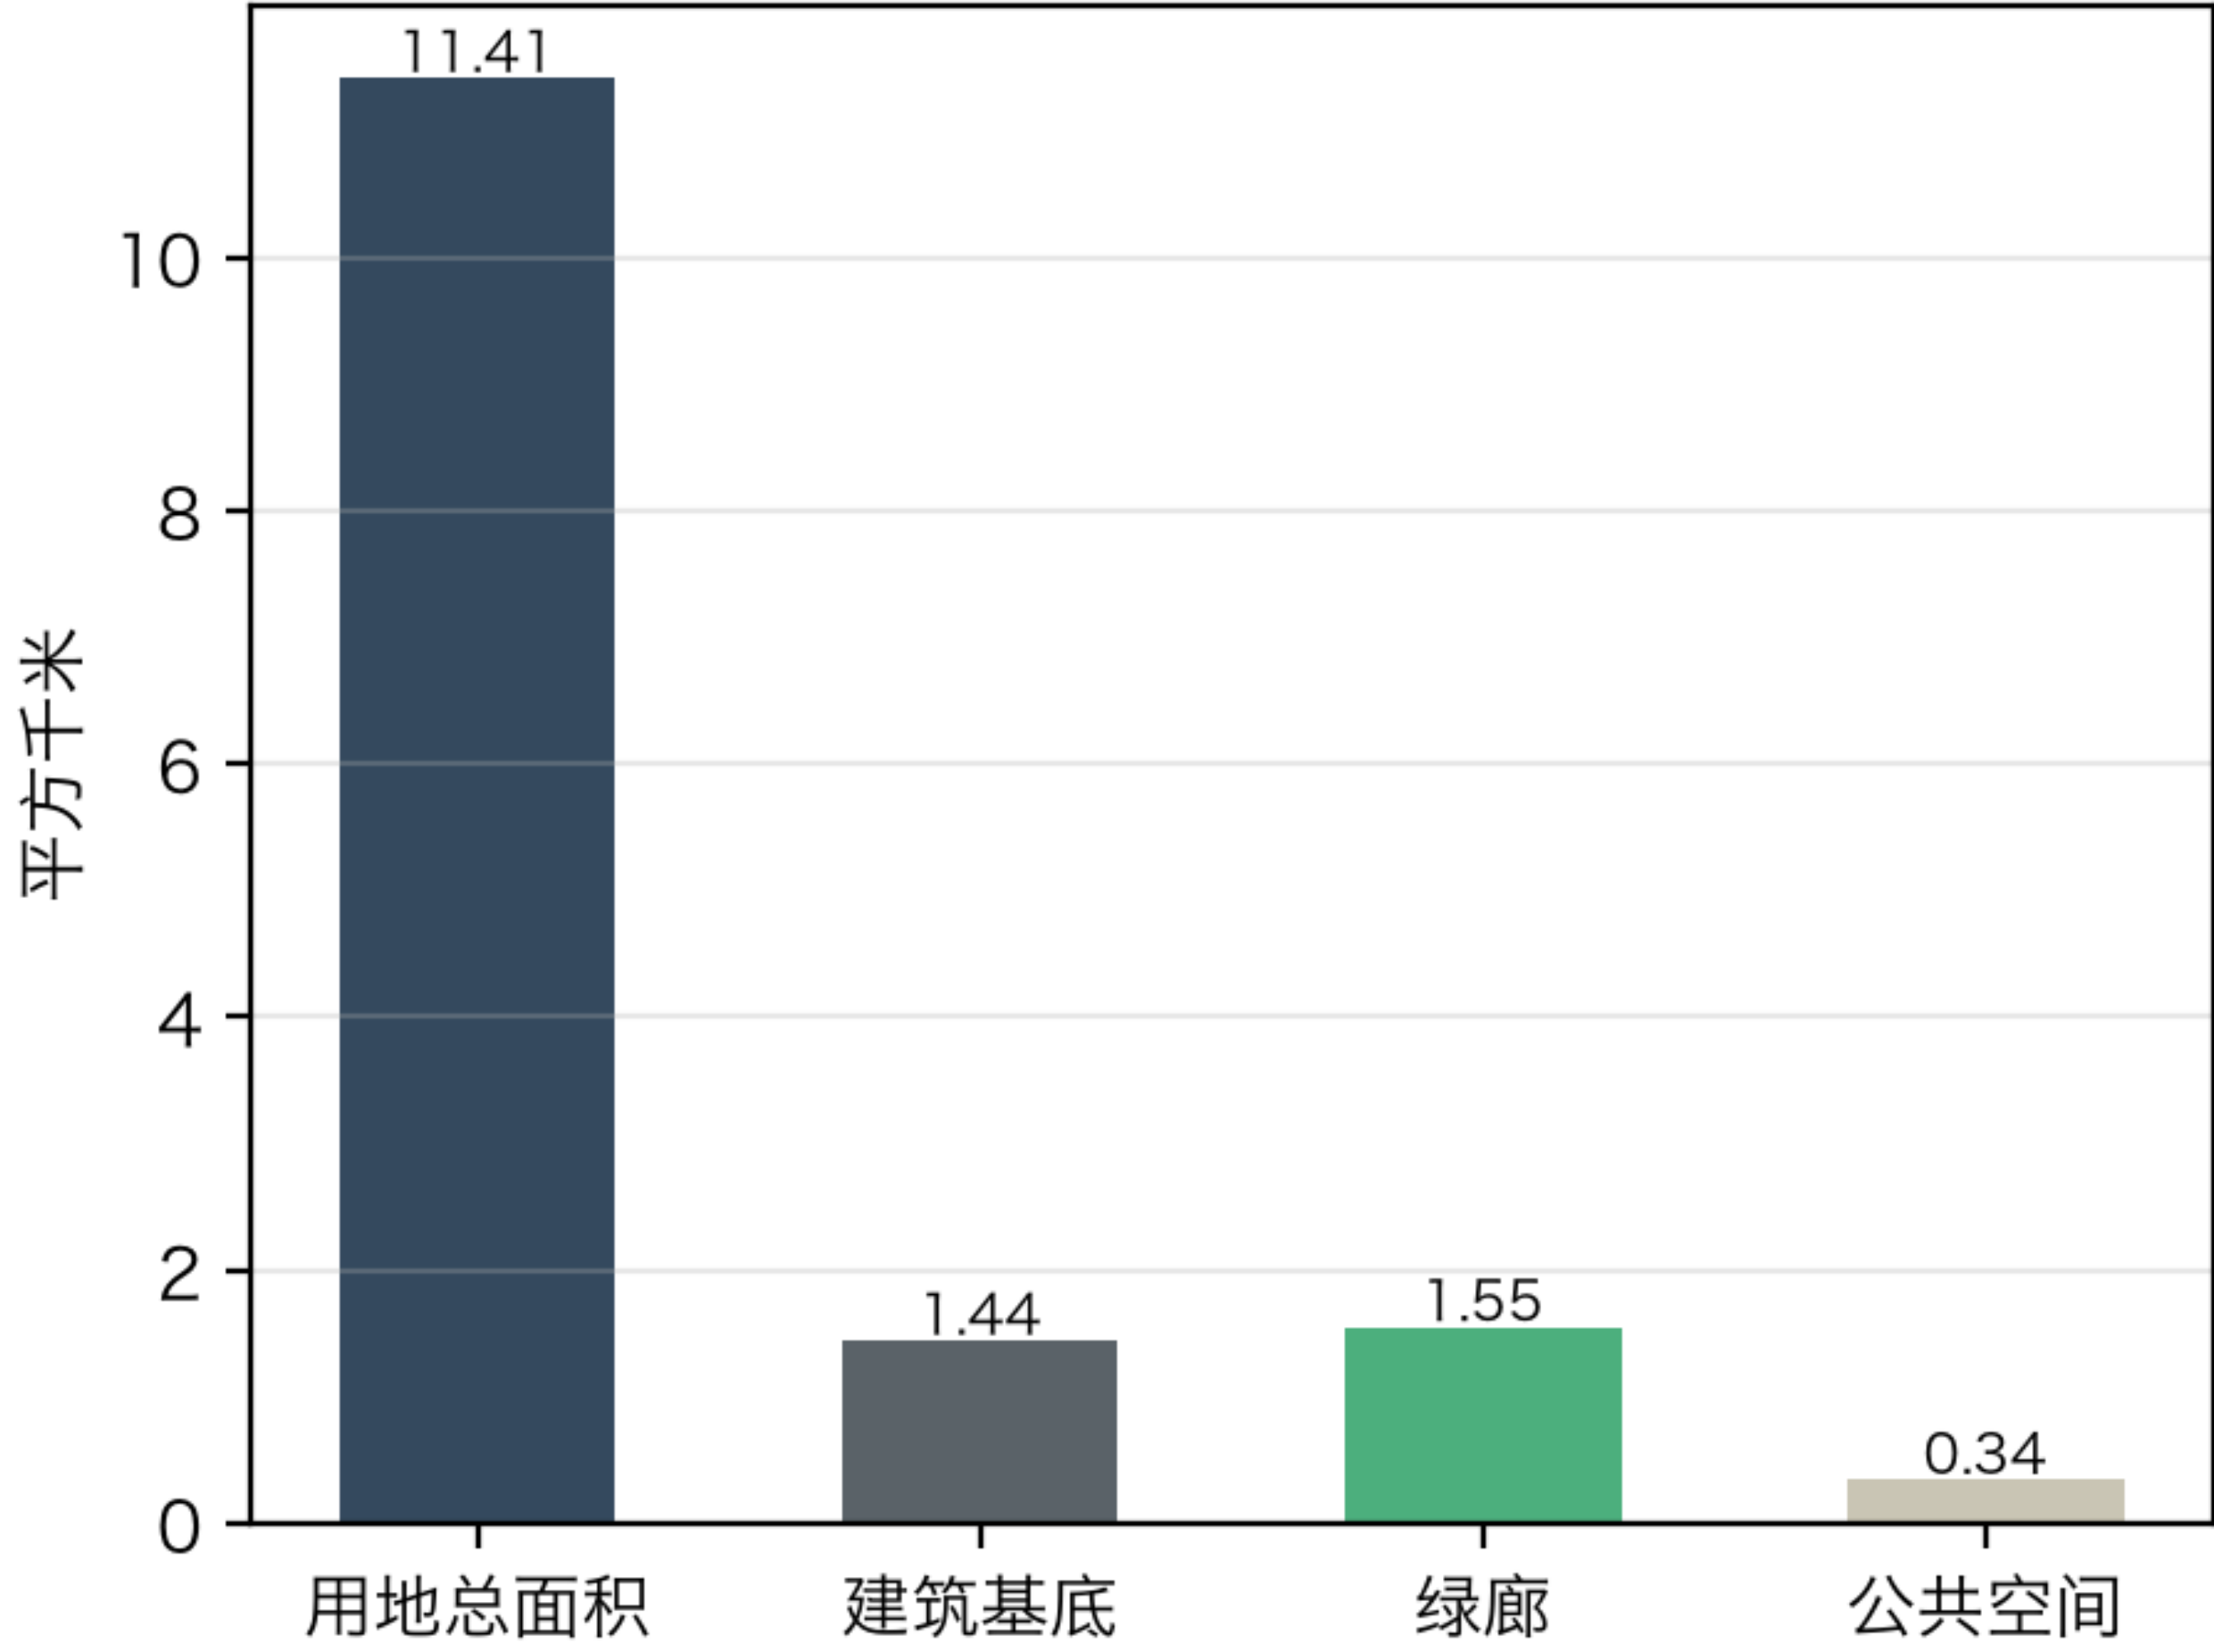


补充指标

- 道路中心线长度: 28,797 m
- 重点区域数量: 3 处
- 近期试点面积(P1): 230 ha

注: 所有面积/比例由提交 GeoJSON 在 EPSG:4548 下复算 (详见 metrics.json), 边界为临时范围。



交通慢行与蓝绿公共空间复合系统

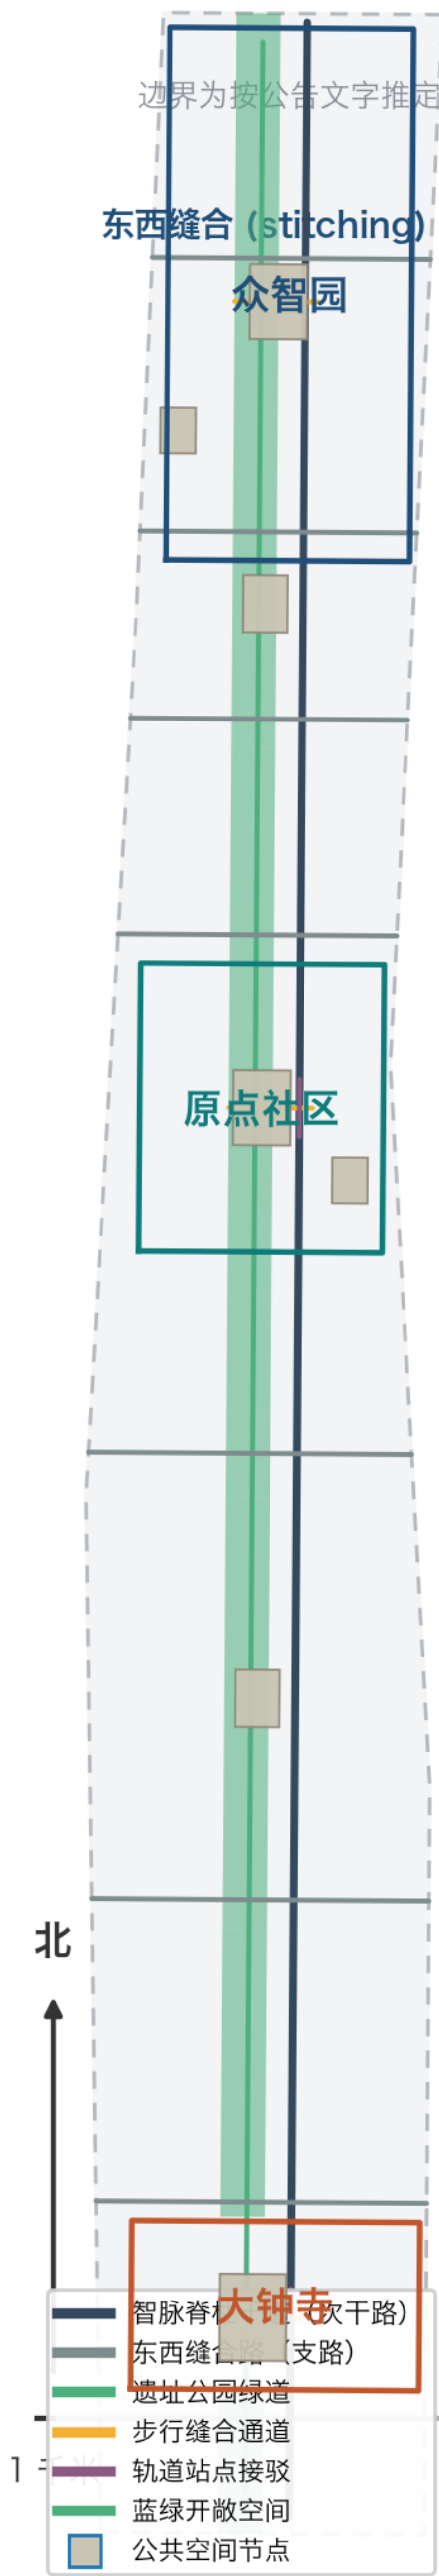



智脉京张 · 总体概念总览

The Belt · Three Cores · Two Wings

